



FGC
Ferrocarrils
de la Generalitat
de Catalunya

Disposició de vies, andanes i senyalització


ENCLAVAMENTS B-V


Aquest document conté:

1 PC_221114.dwg	14/11/2022	Esquema enclavament Plaça Catalunya
2 GR_221115.dwg	15/11/2022	Esquema enclavament Gràcia
3 GR_221115.dwg	15/11/2022	Esquema enclavament Gràcia_2ª Part
4 SR_230217.dwg	17/02/2023	Esquema enclavament Sarrià
5 SR_230217.dwg	17/02/2023	Esquema enclavament Sarrià
6 LP_220509.dwg	09/05/2022	Esquema enclavament Les Planes
7 LF_221007.dwg	07/10/2022	Esquema enclavament La Floresta
8 SC_221122.dwg	22/11/2022	Esquema enclavament Sant Cugat
9 RB_COR_220601.dwg	01/06/2022	Esquema enclavament RUBI - COR
10 RB_220427.dwg	27/04/2022	Esquema enclavament RUBI
11 FN_220609.dwg	09/06/2022	Esquema enclavament Les Fonts de Terrassa
12 TR_220425.dwg	25/04/2022	Esquema enclavament Terrassa
13 NA_220513.dwg	13/05/2022	Esquema enclavament Nacions Unides
14 VO_220426.dwg	26/04/2022	Esquema enclavament Volpelleres
15 UN_221129.dwg	29/11/2022	Esquema enclavament Universitat Autònoma
16 CF_221125.dwg	25/11/2022	Esquema enclavament Can Feu Gràcia
17 NO_200121.dwg	21/01/2020	Esquema enclavament Sabadell Nord
18 PN_220527.dwg	27/05/2022	Esquema enclavament Sabadell Parc del Nord


Ref: ENCLAVAMENTS B-V.xls


Barcelona, 20 de febrer de 2023

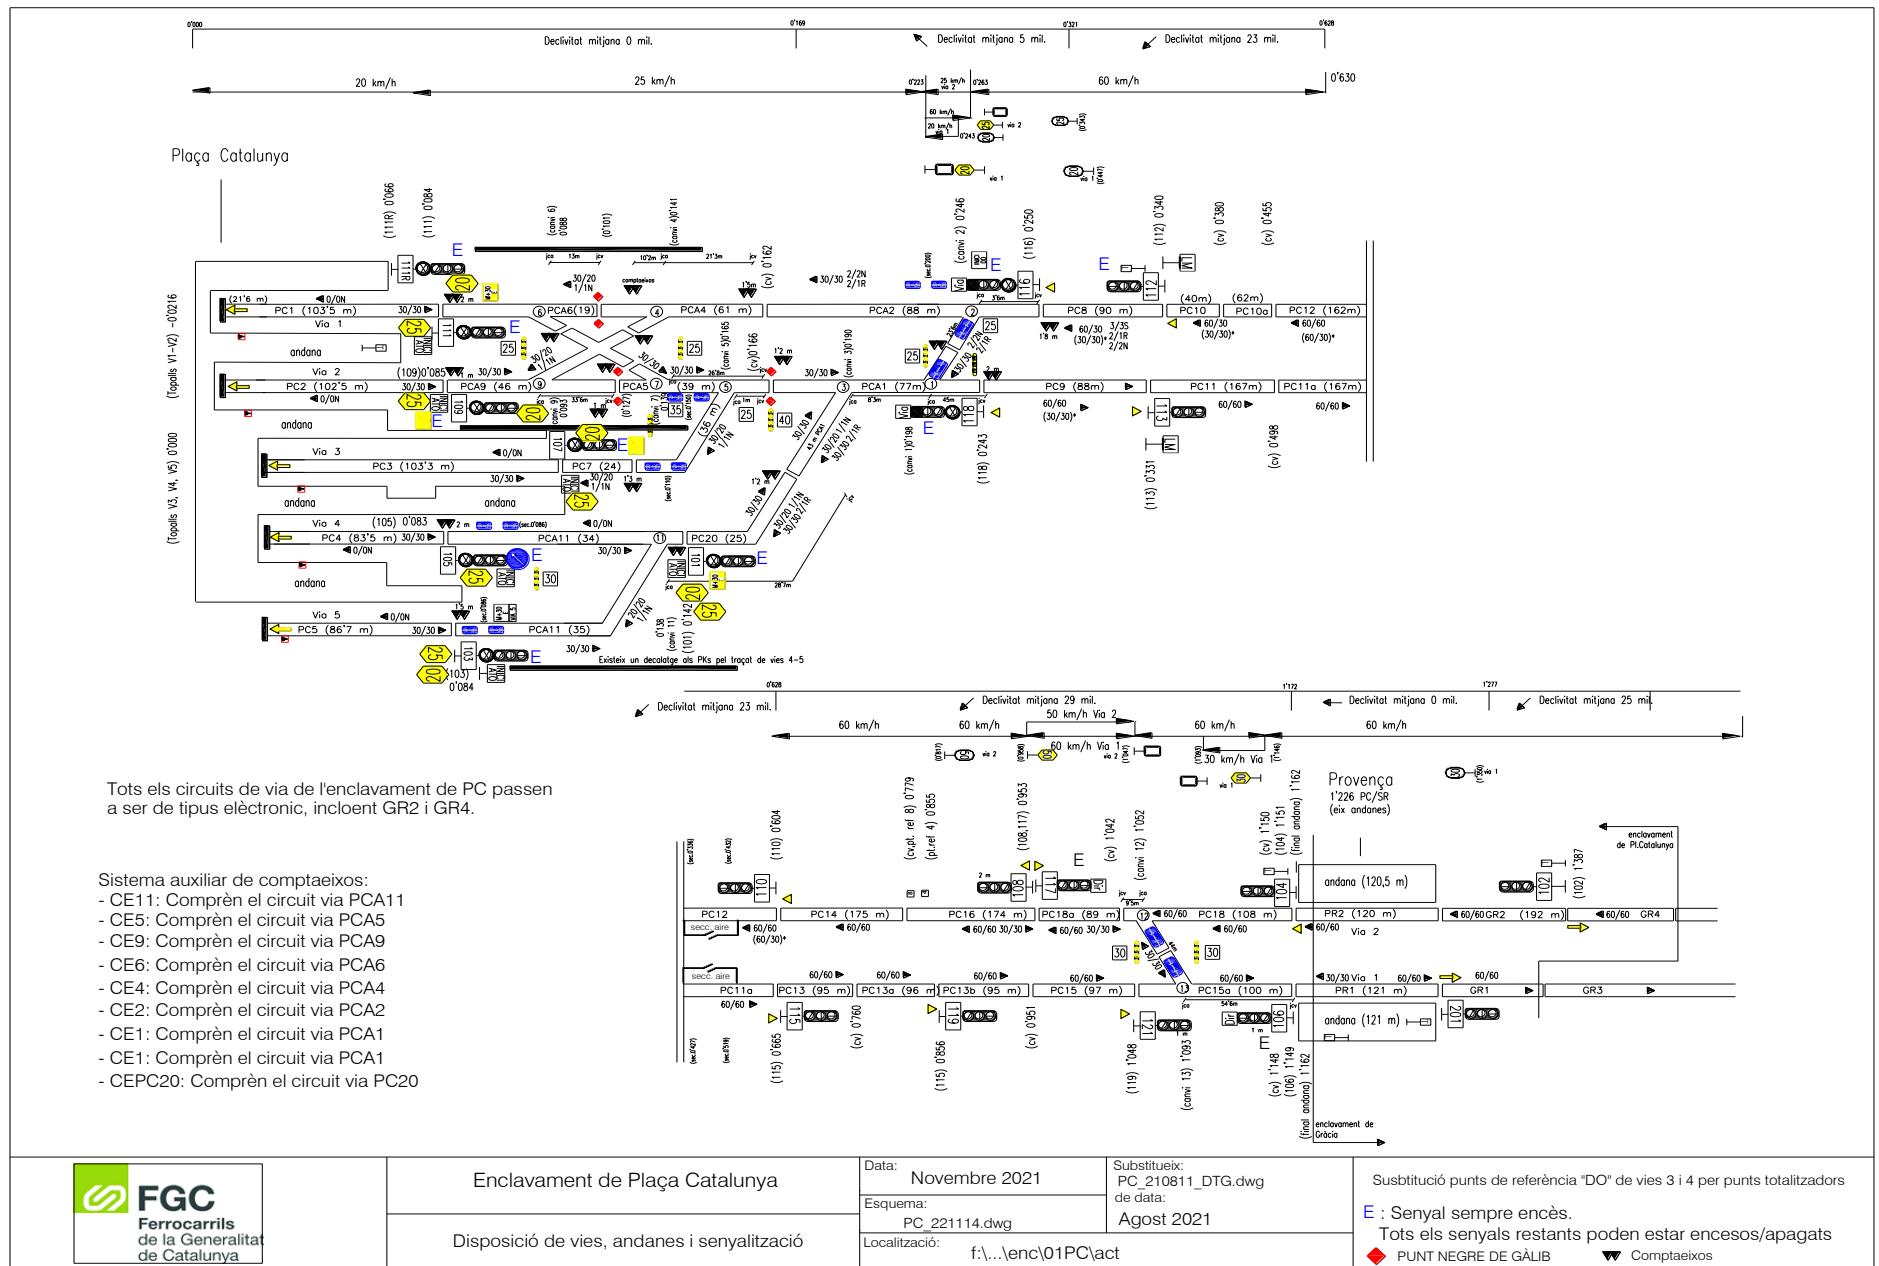

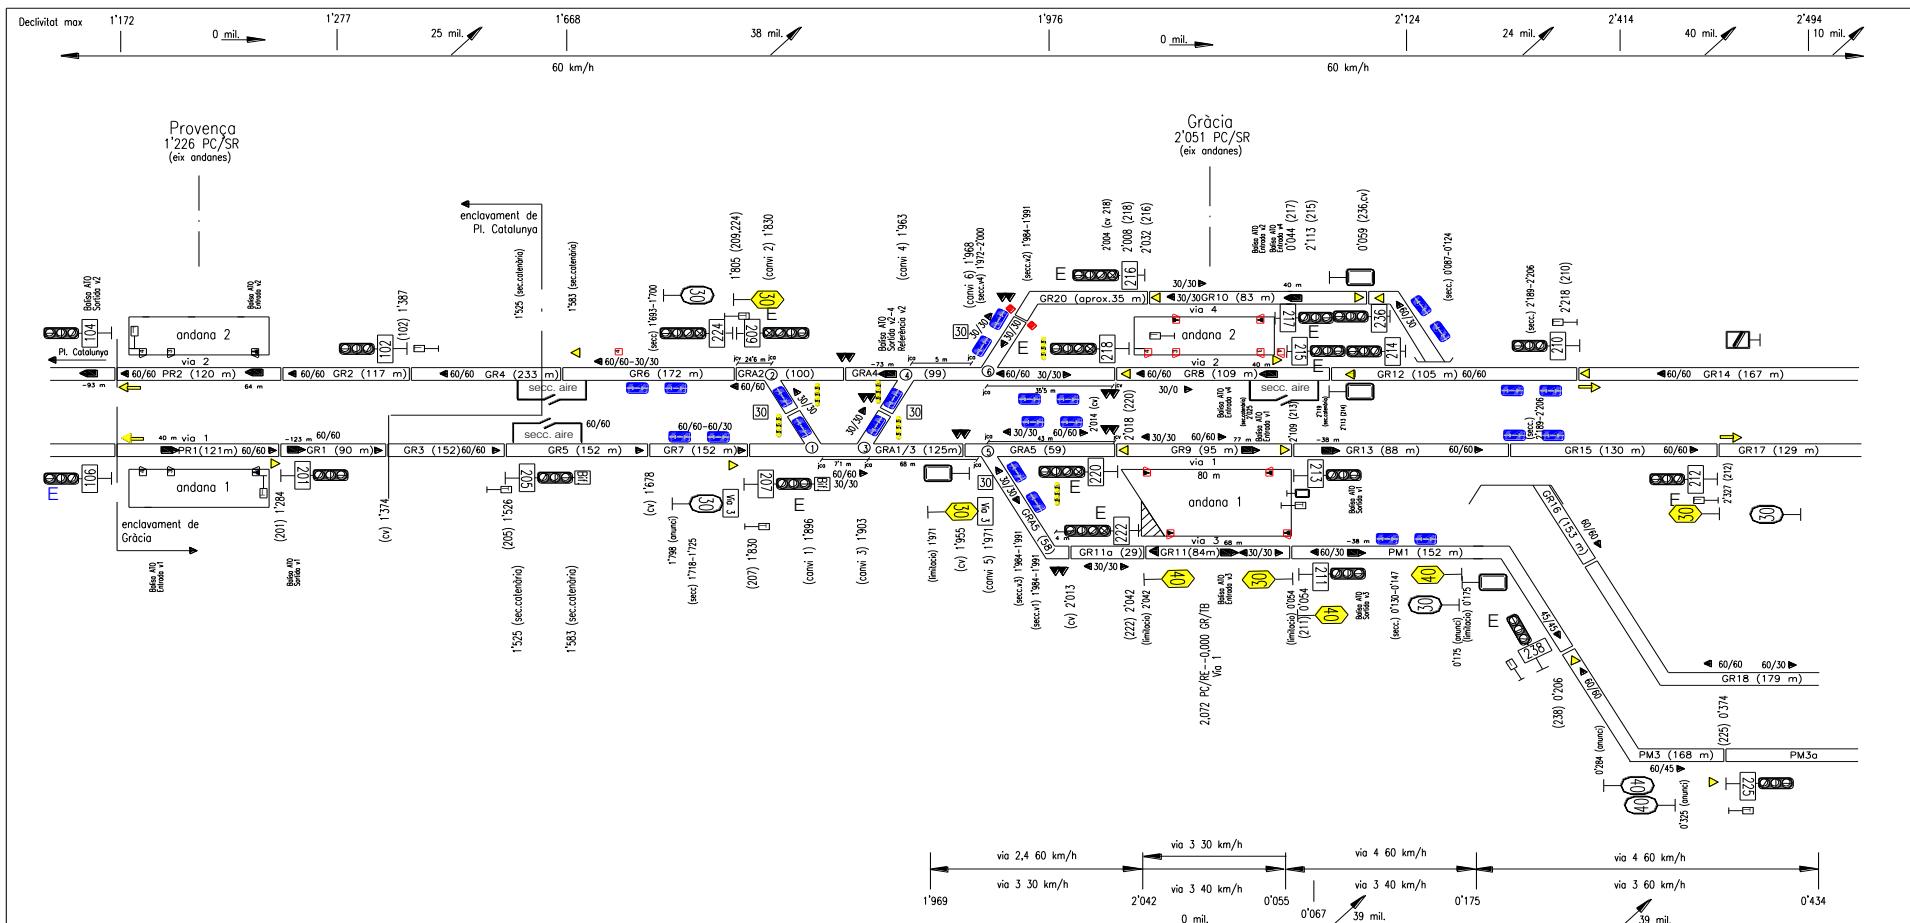

FGC Ferrocarrils de la Generalitat de Catalunya	Enclavament de Gràcia Disposició de vies, andanes i senyalització	Data: Novembre de 2022 Esquema: GR_221115.dwg Localització: <code>f:\...\enc\02gr\</code>	Substitueix: GR_220506.dwg de data: Maig de 2022	Baixa senyals INICI/FINAL ATO a Gràcia
				◆ PUNT NEGRE DE GÀLIB
				■ Senyal sempre ences

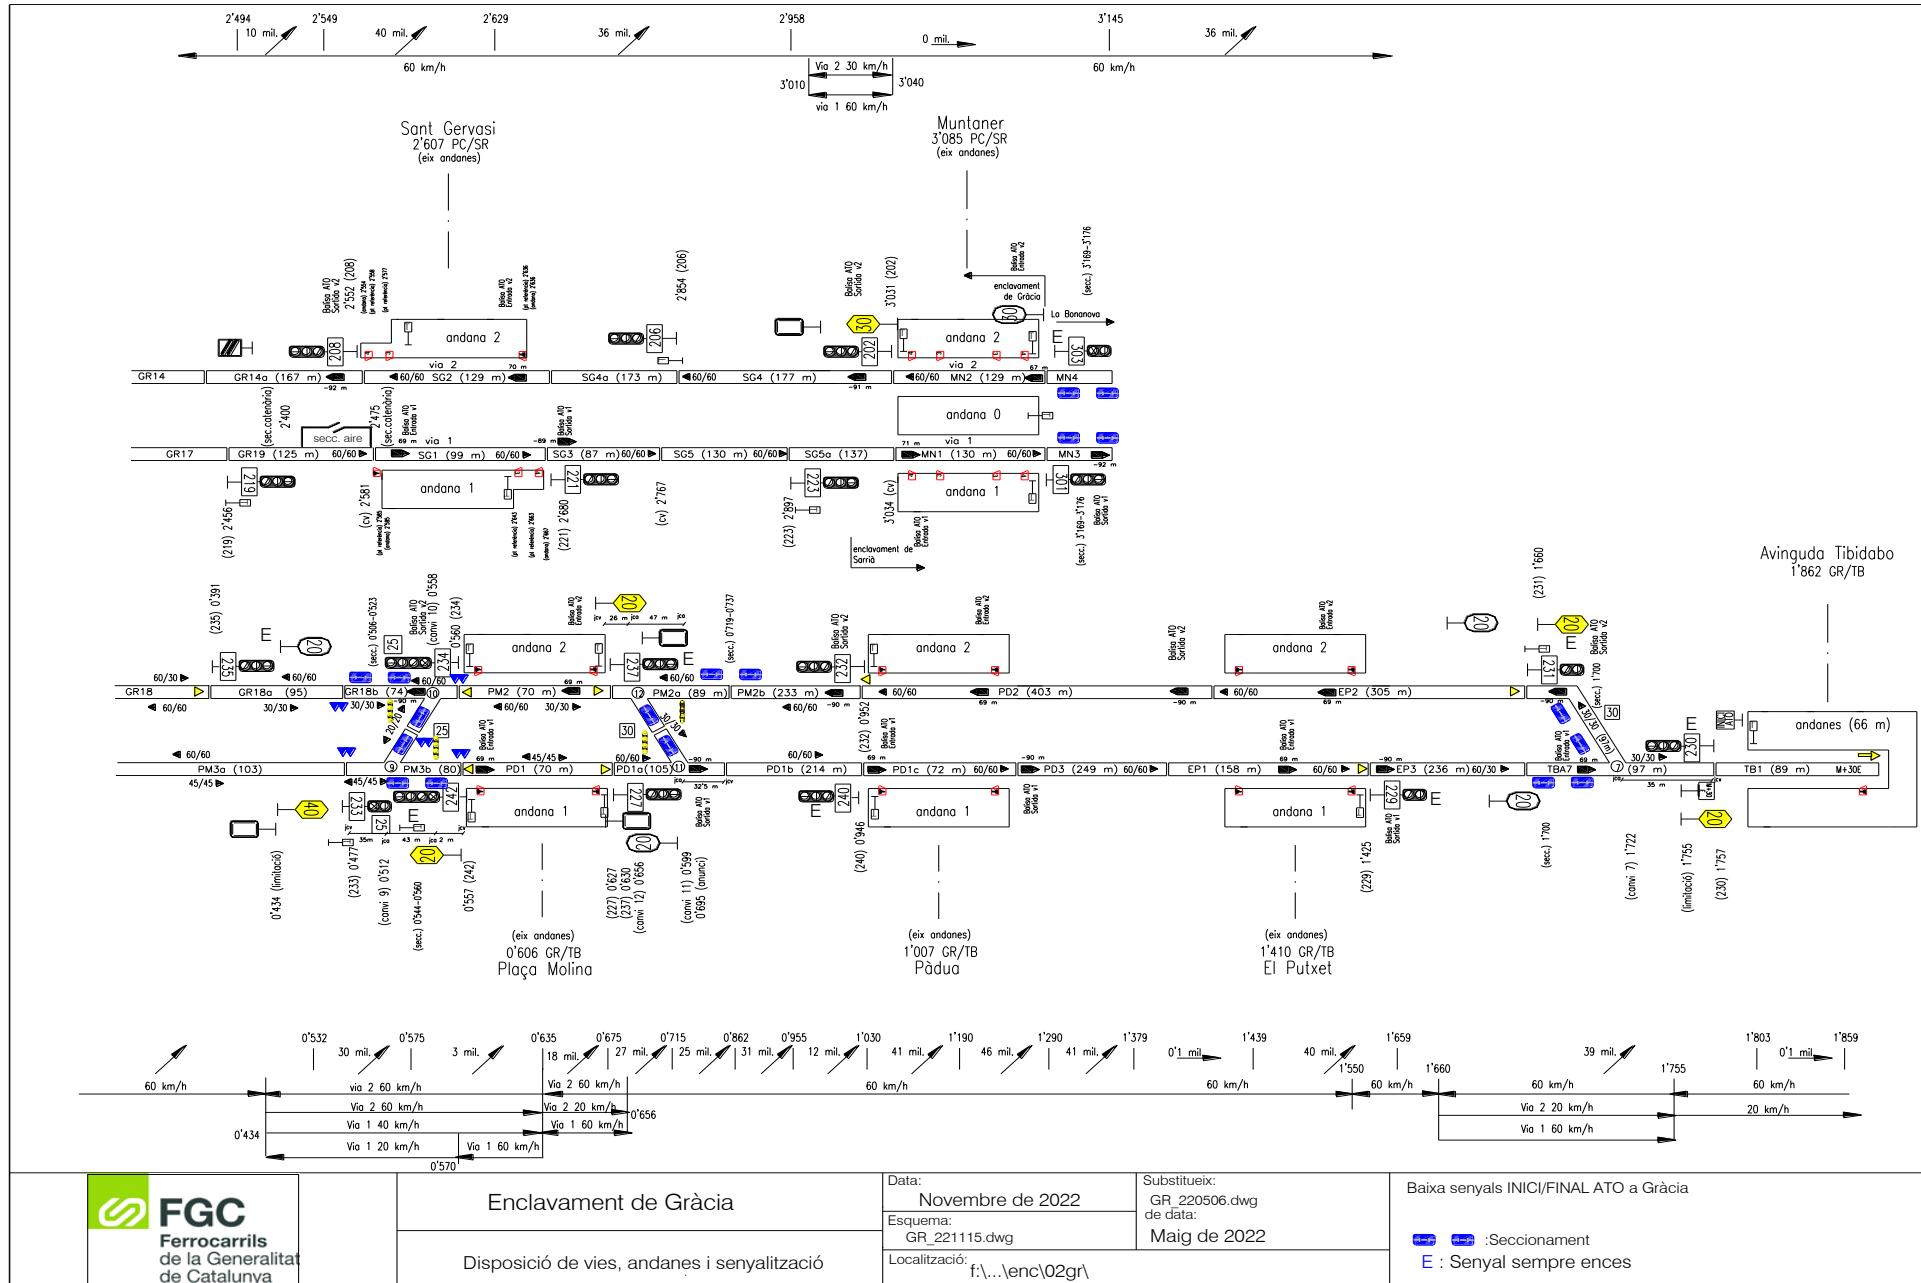

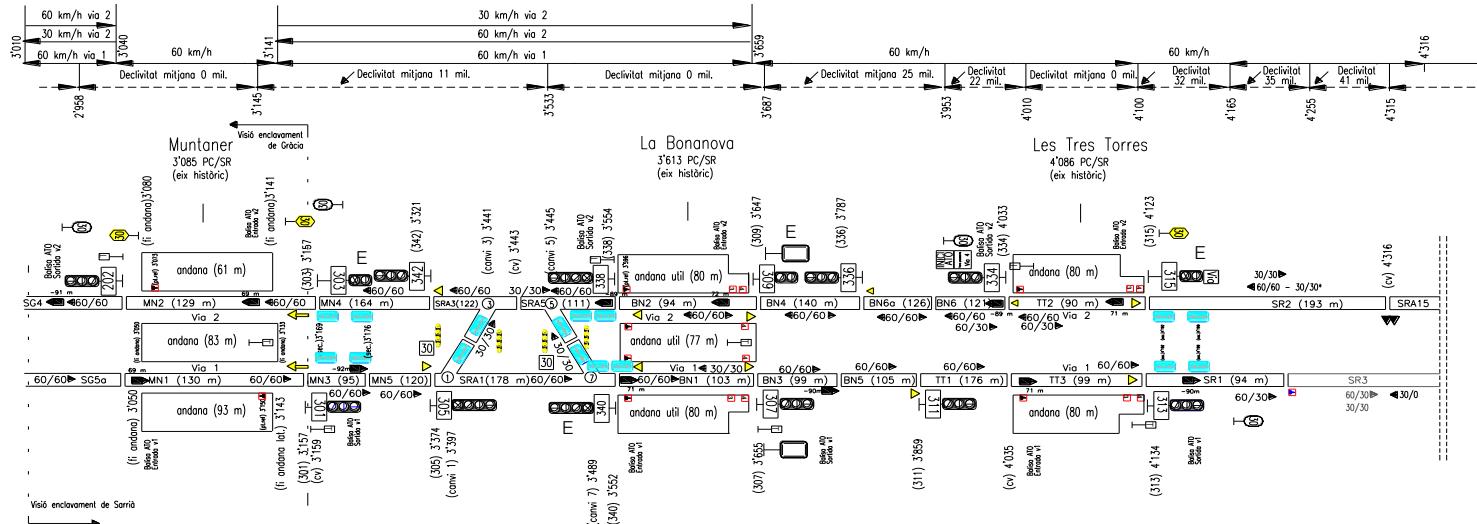

Enclavament de Sarrià

Disposició de vies, andanes i senyalització

Data: Februar 2023

Esquema:

SR_230217.dwg

Localització: f:\...\enc\BVSR


Substitueix:
SR 221209.dwg


de data:


Desembre 2022


Substitució temporal senyal "INICI ATO Via 1" per "INICI ATP" a via 4 SR
Substitució temporal punts referència ascendent andanes RE


For more information about the study, please contact Dr. Michael J. Hwang at (310) 794-3000 or via email at mhwang@ucla.edu.

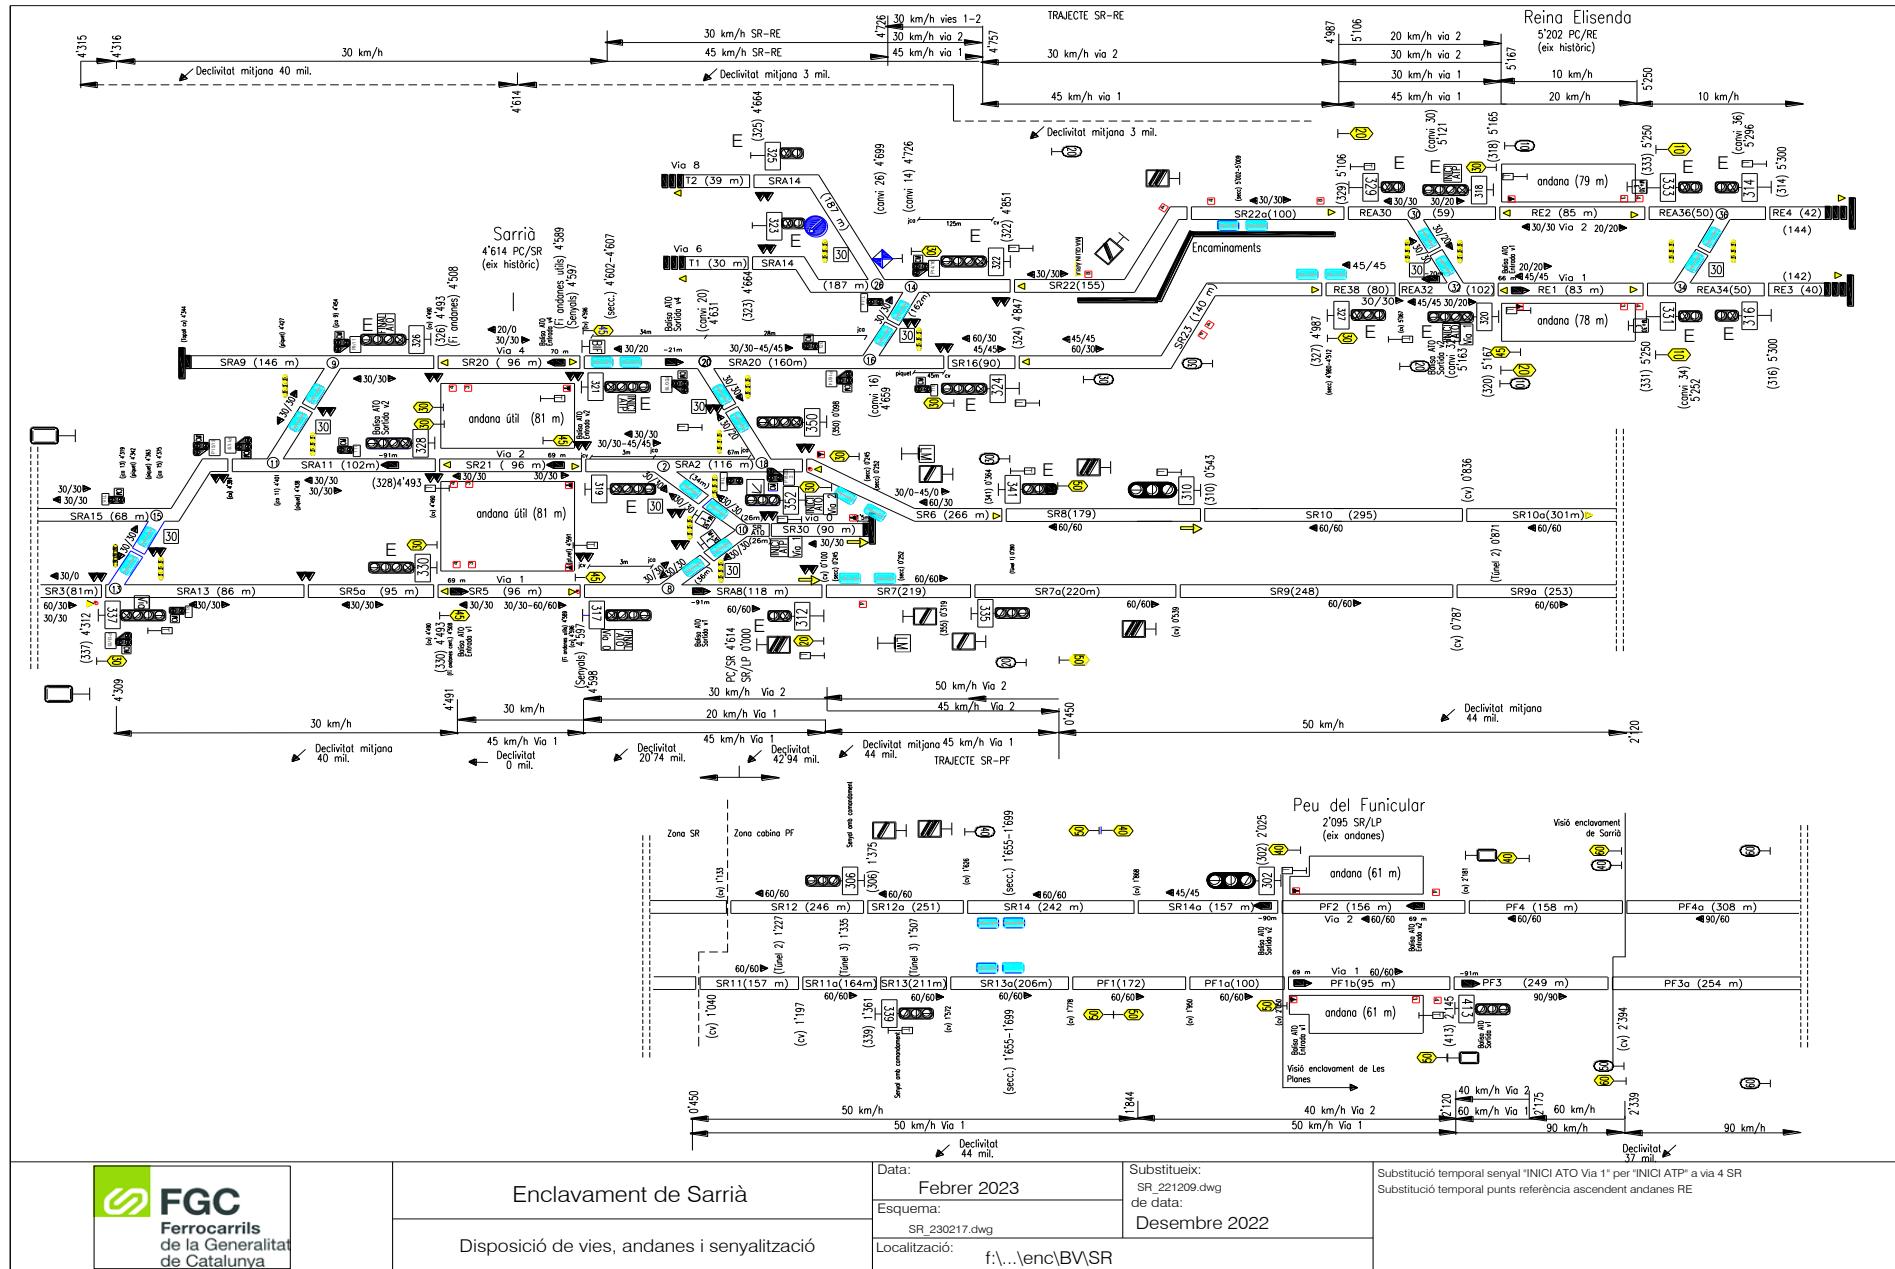

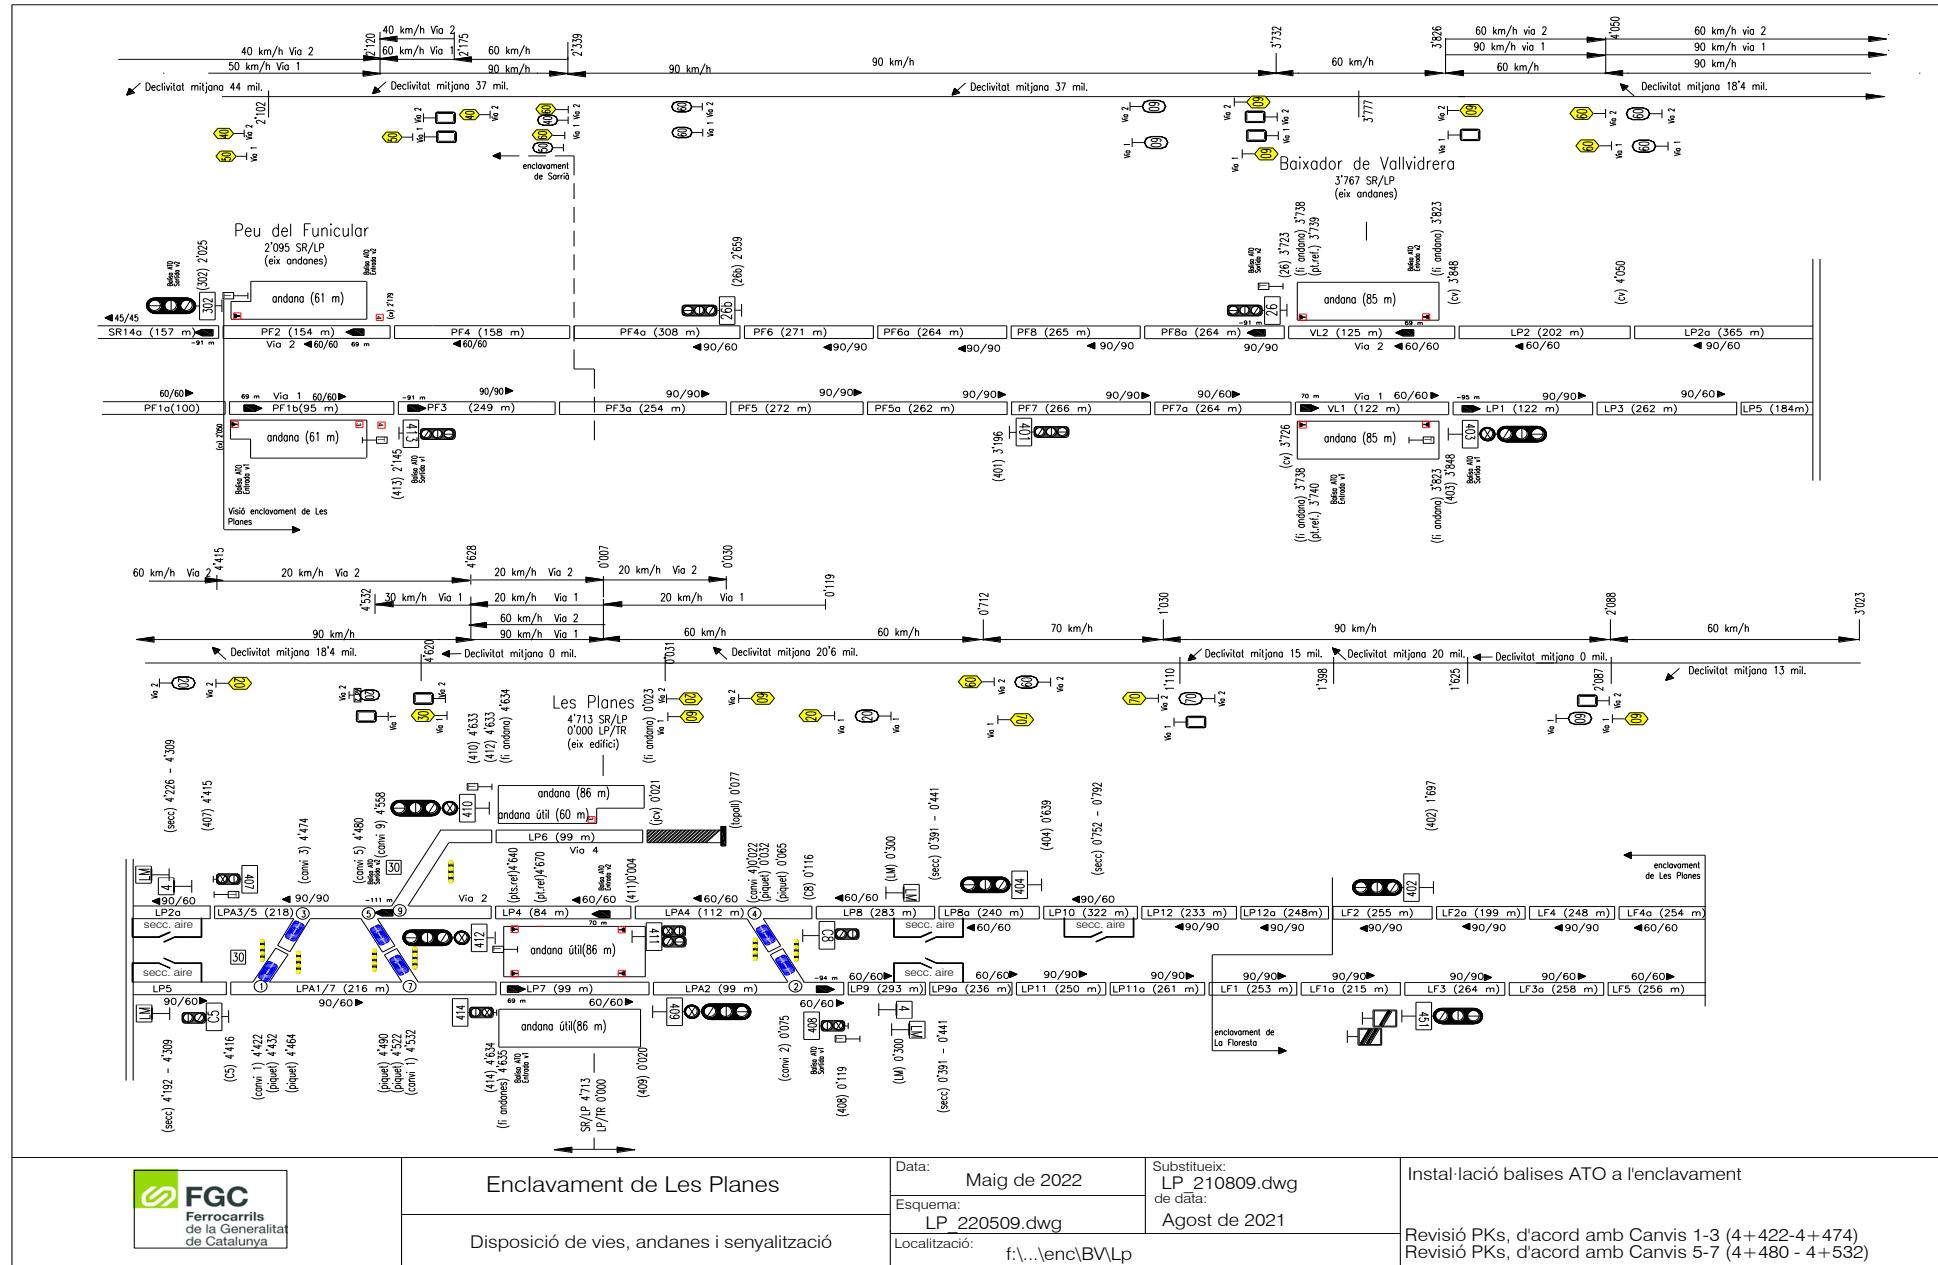

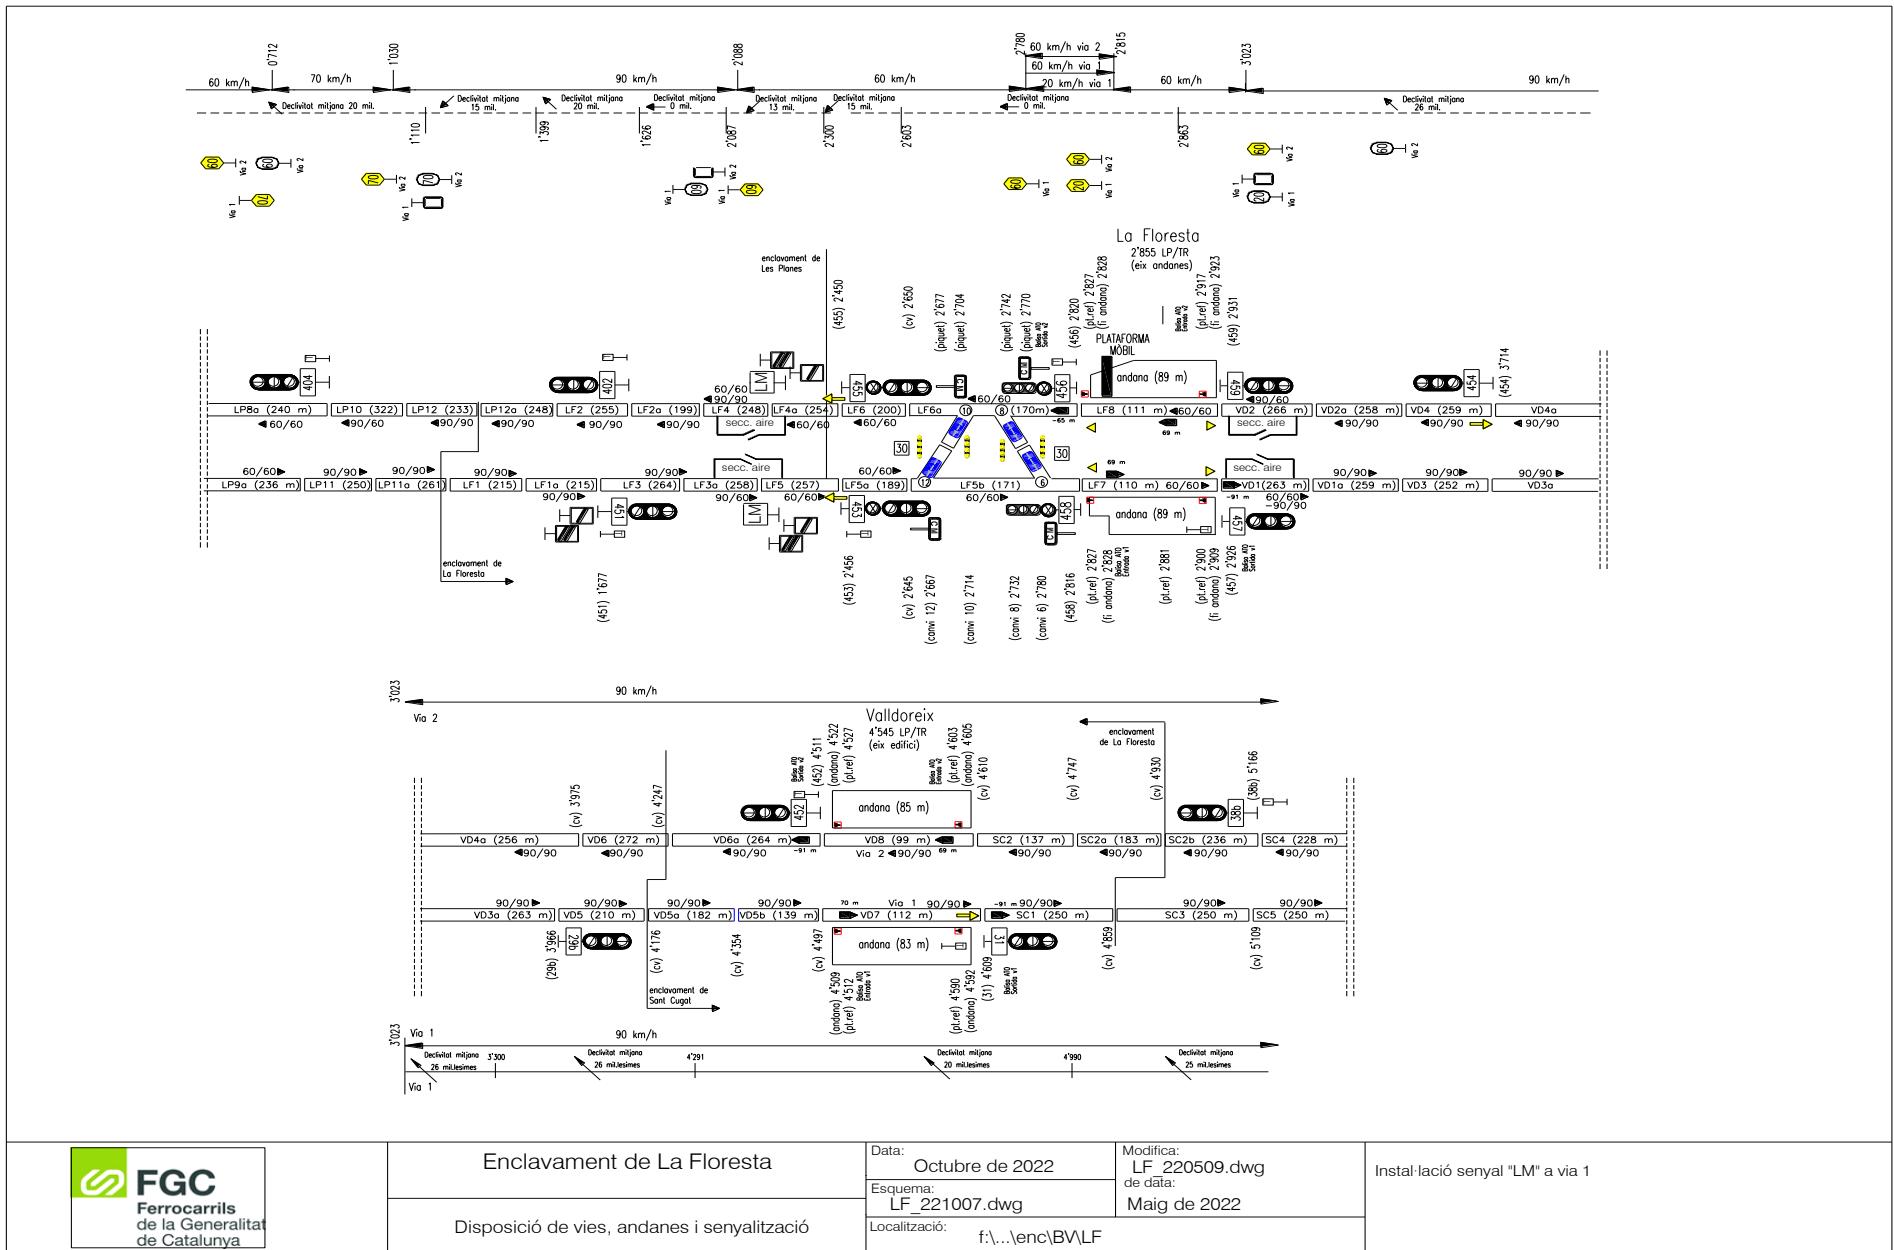

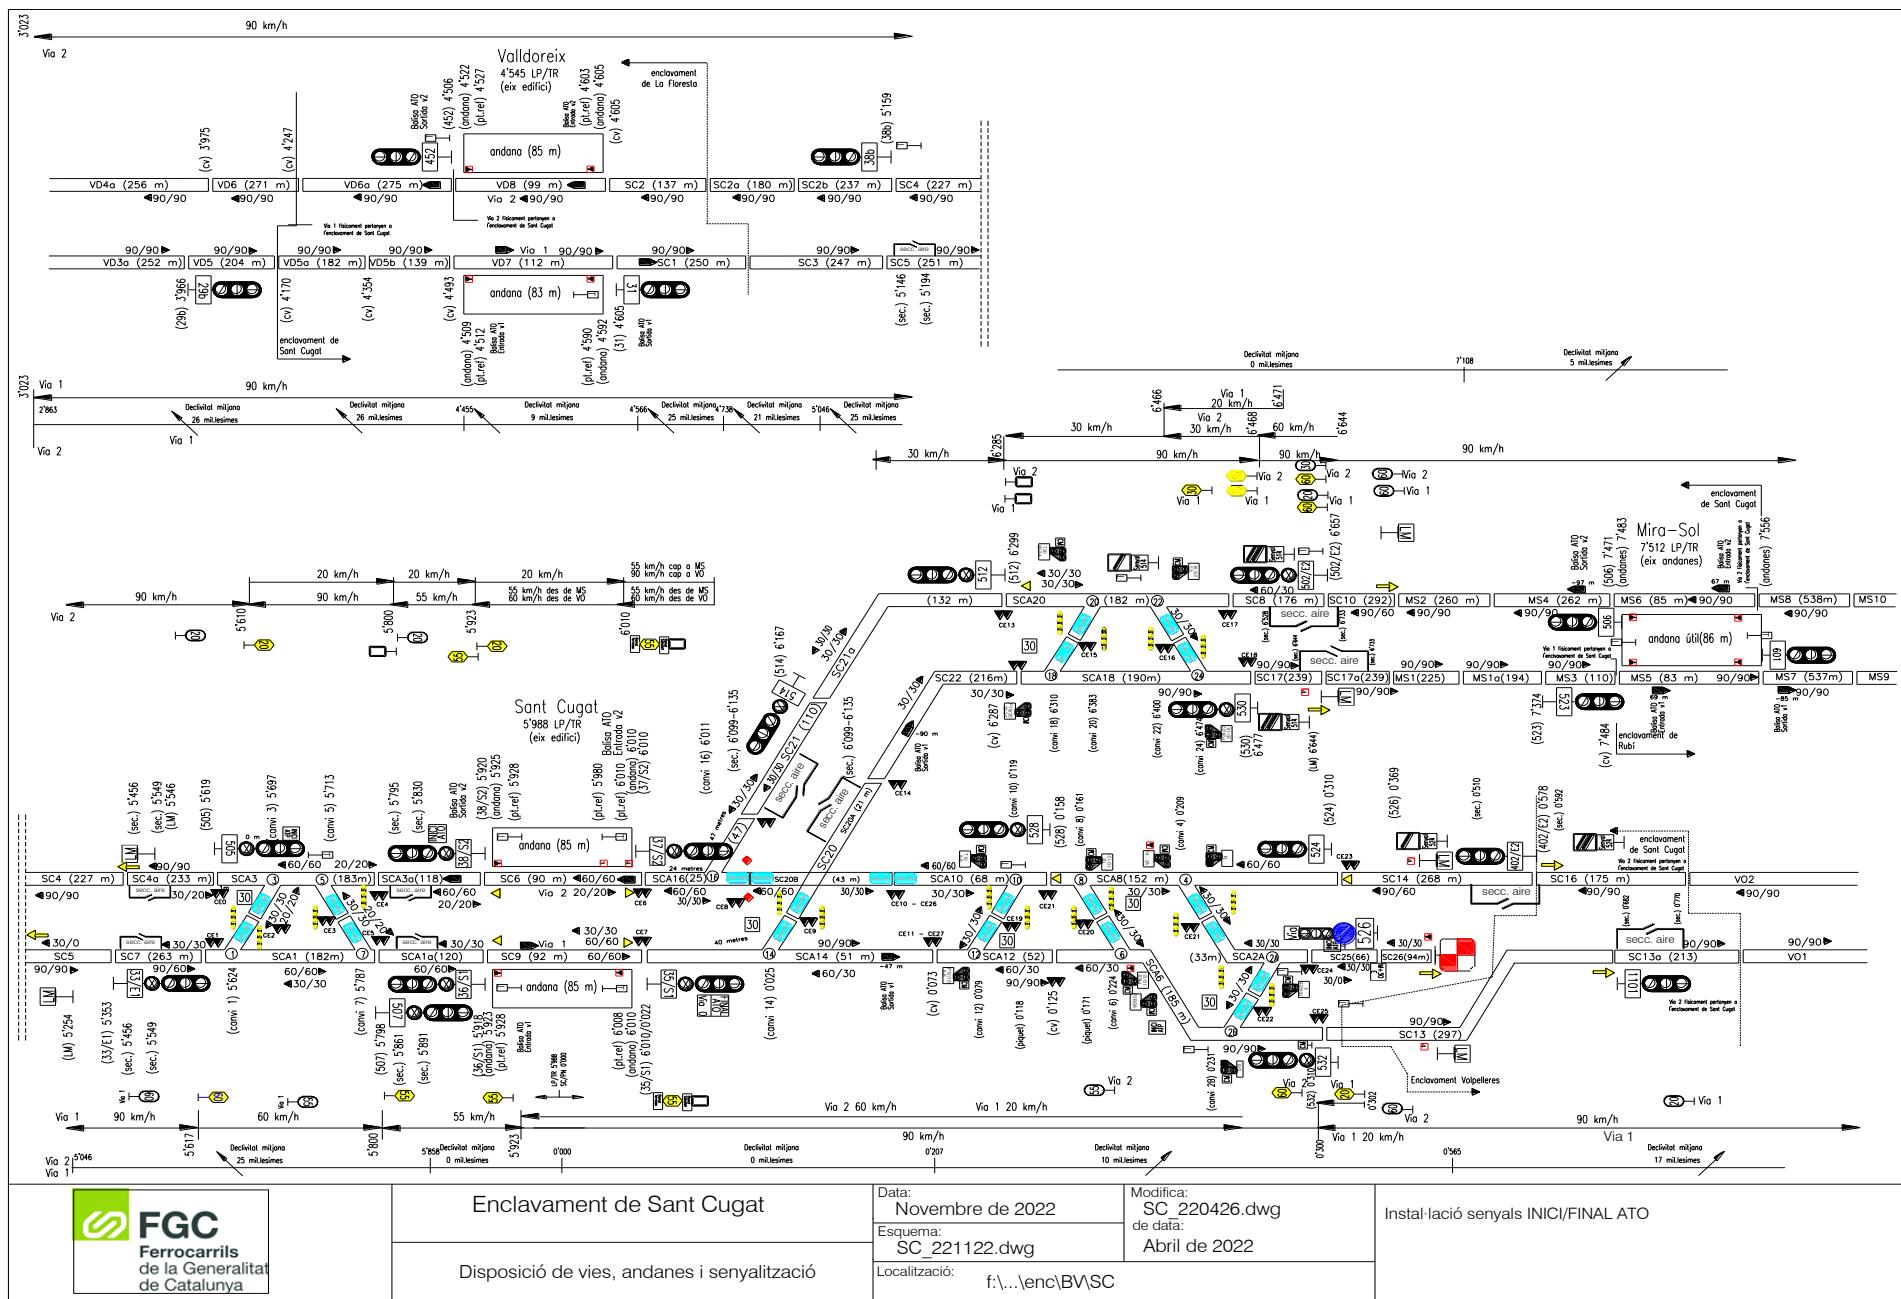

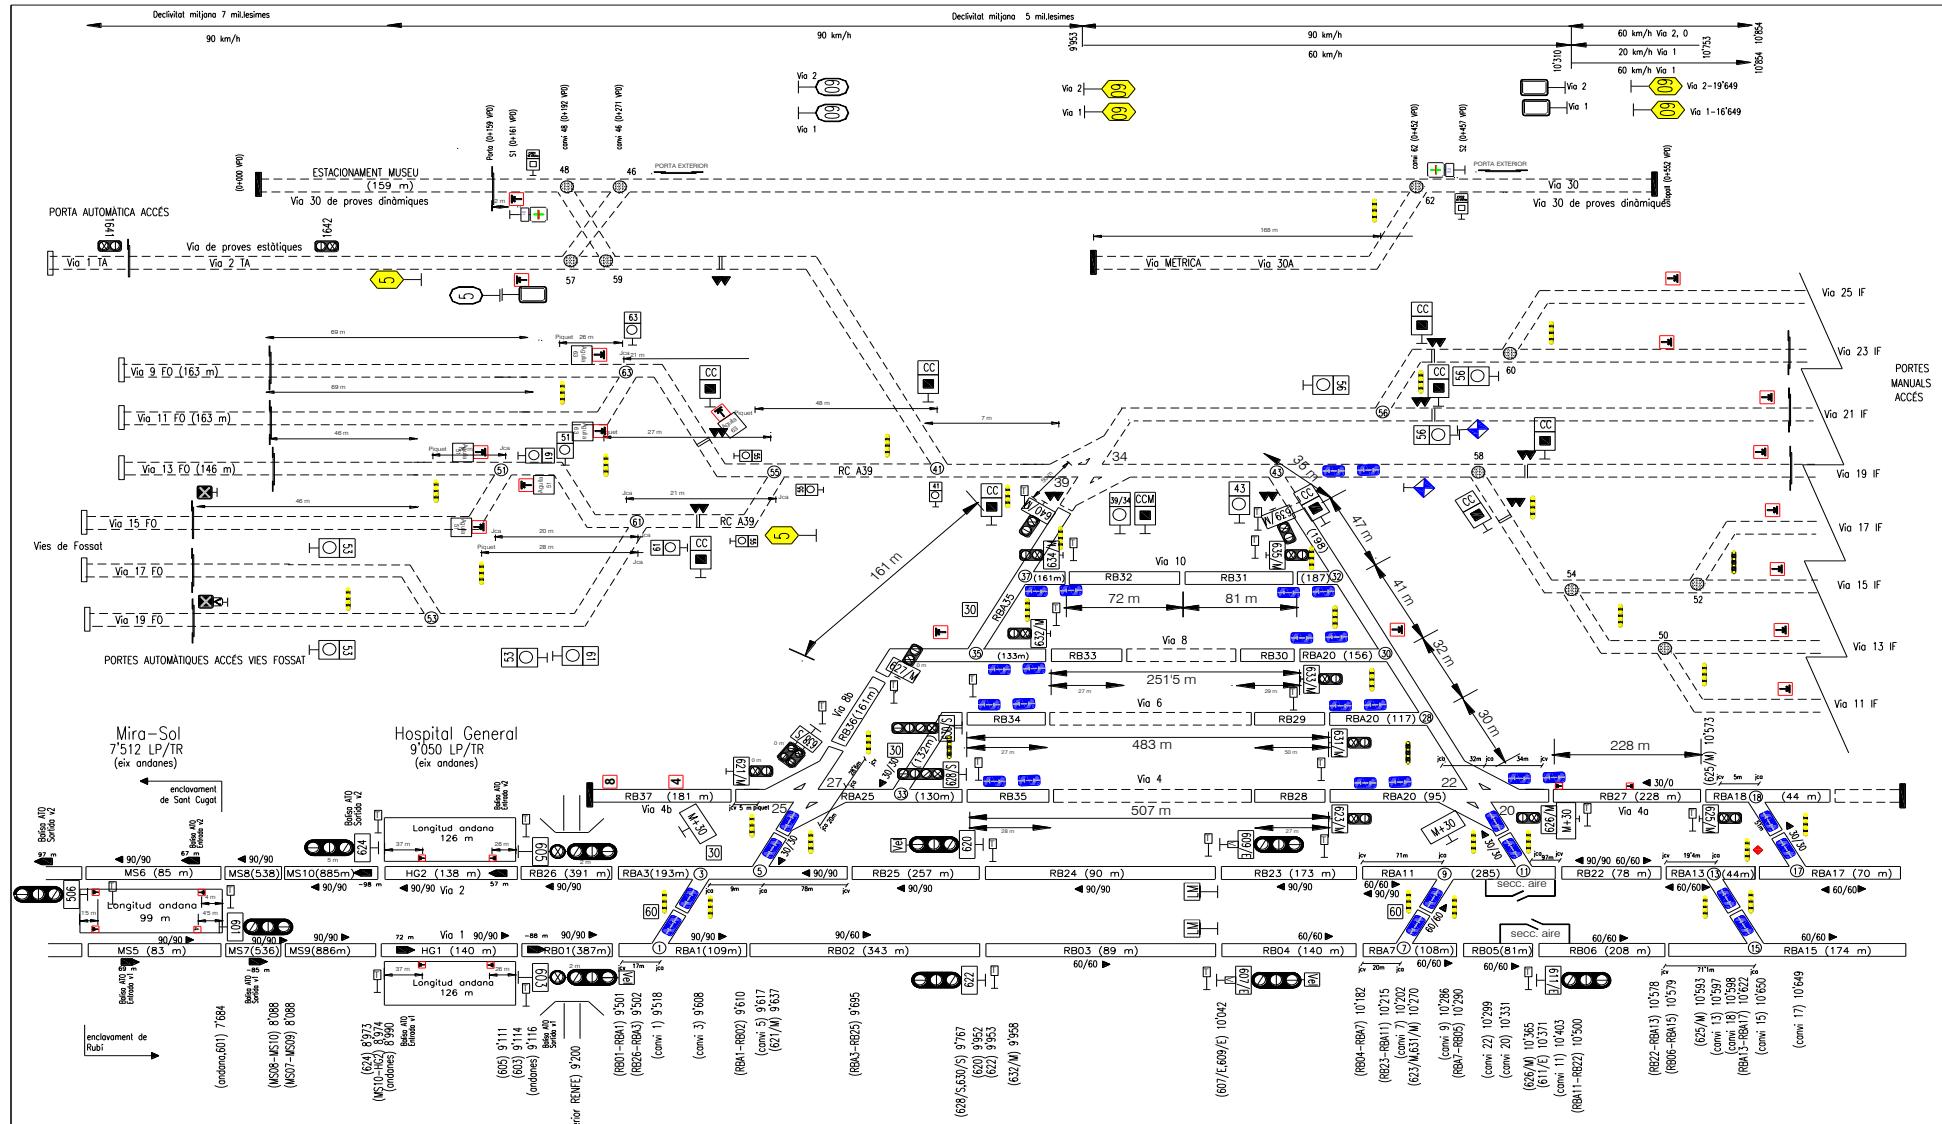

FGC
Ferrocarrils
de la Generalitat
de Catalunya


Enclavament de Rubí


Esquemàtic disposició de vies, canvis d'agulles,
secciónaments i senyalització


Data: Juni de 2022	Substitueix: RB COR_220518.dwg de data: Maig de 2022
Esquema: RB COR_220601.dwg	
Doc.Rel:	


Revisió situació estacionaments del COR, vies 4, 6, 8 i 10. Modificació estacionament via 4b.
Alta noves vies 9, 11 i 13 de Tallers. Instalació balises ATO a MS i HG.
Desplaçament i canvi de mà del senyal 621/M
Caixes de comandament de maniobres zona TUD 34/39
Caixa de Control Maniobres zona TUD 34/39
▼ Comptafeixos




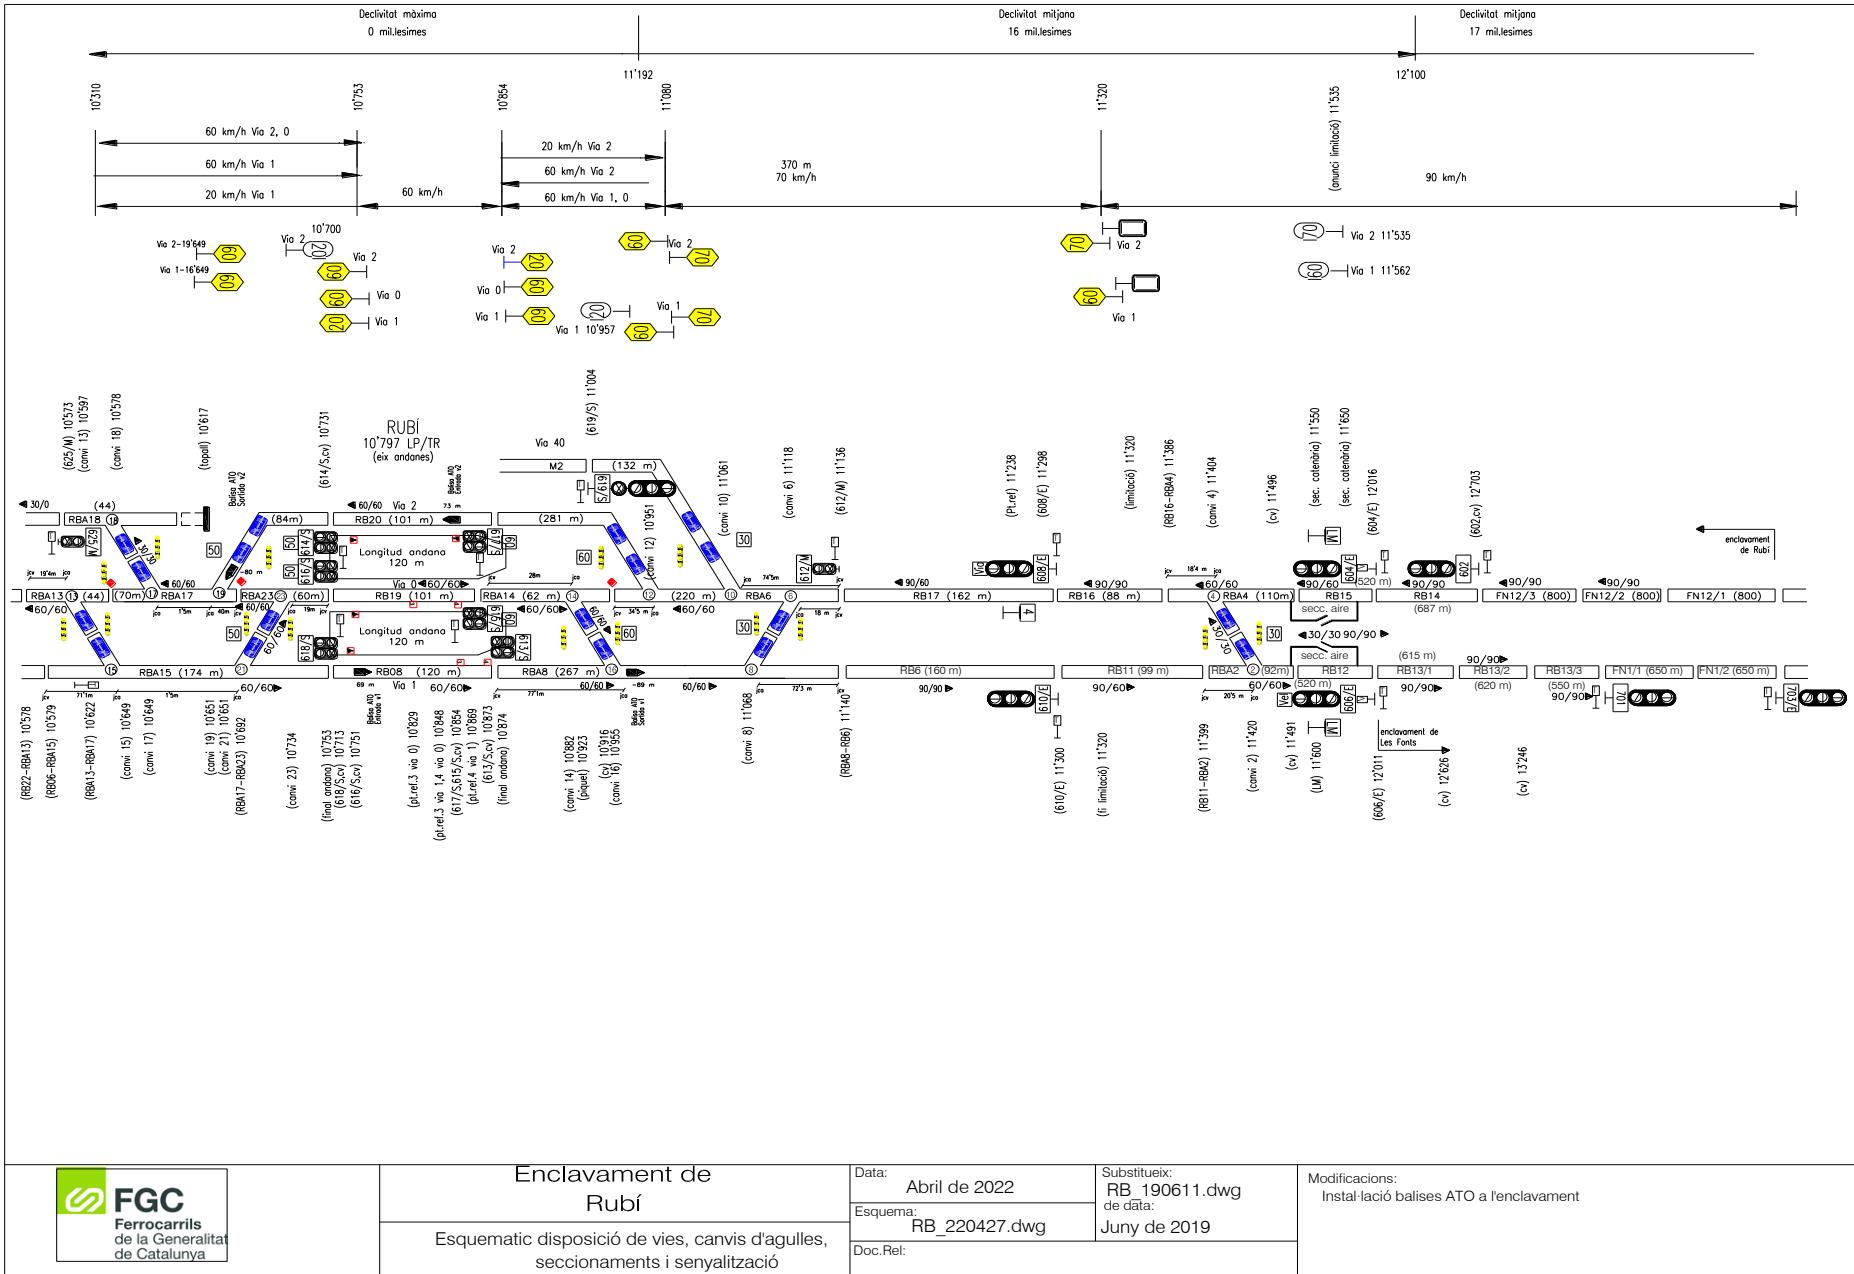


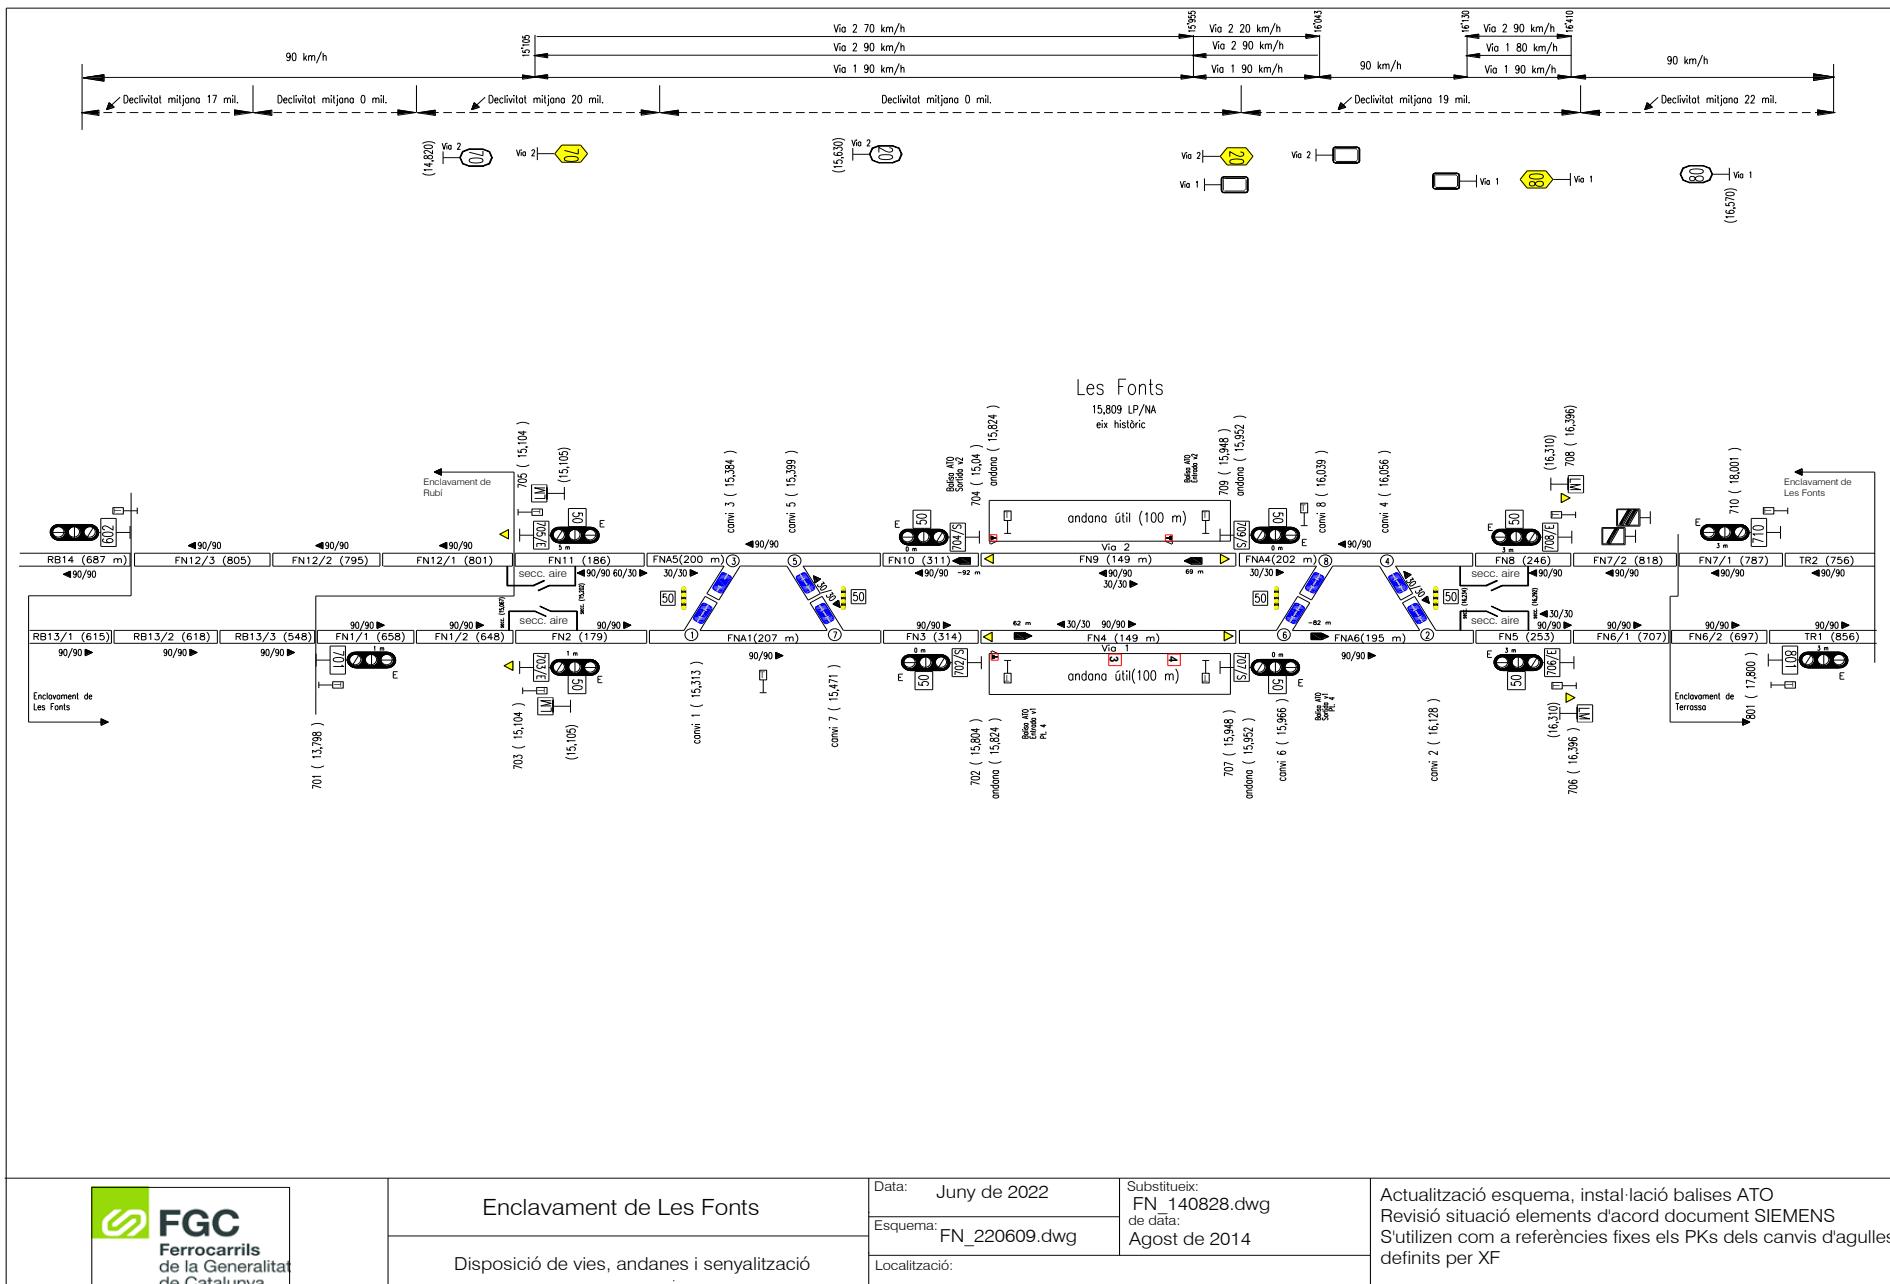


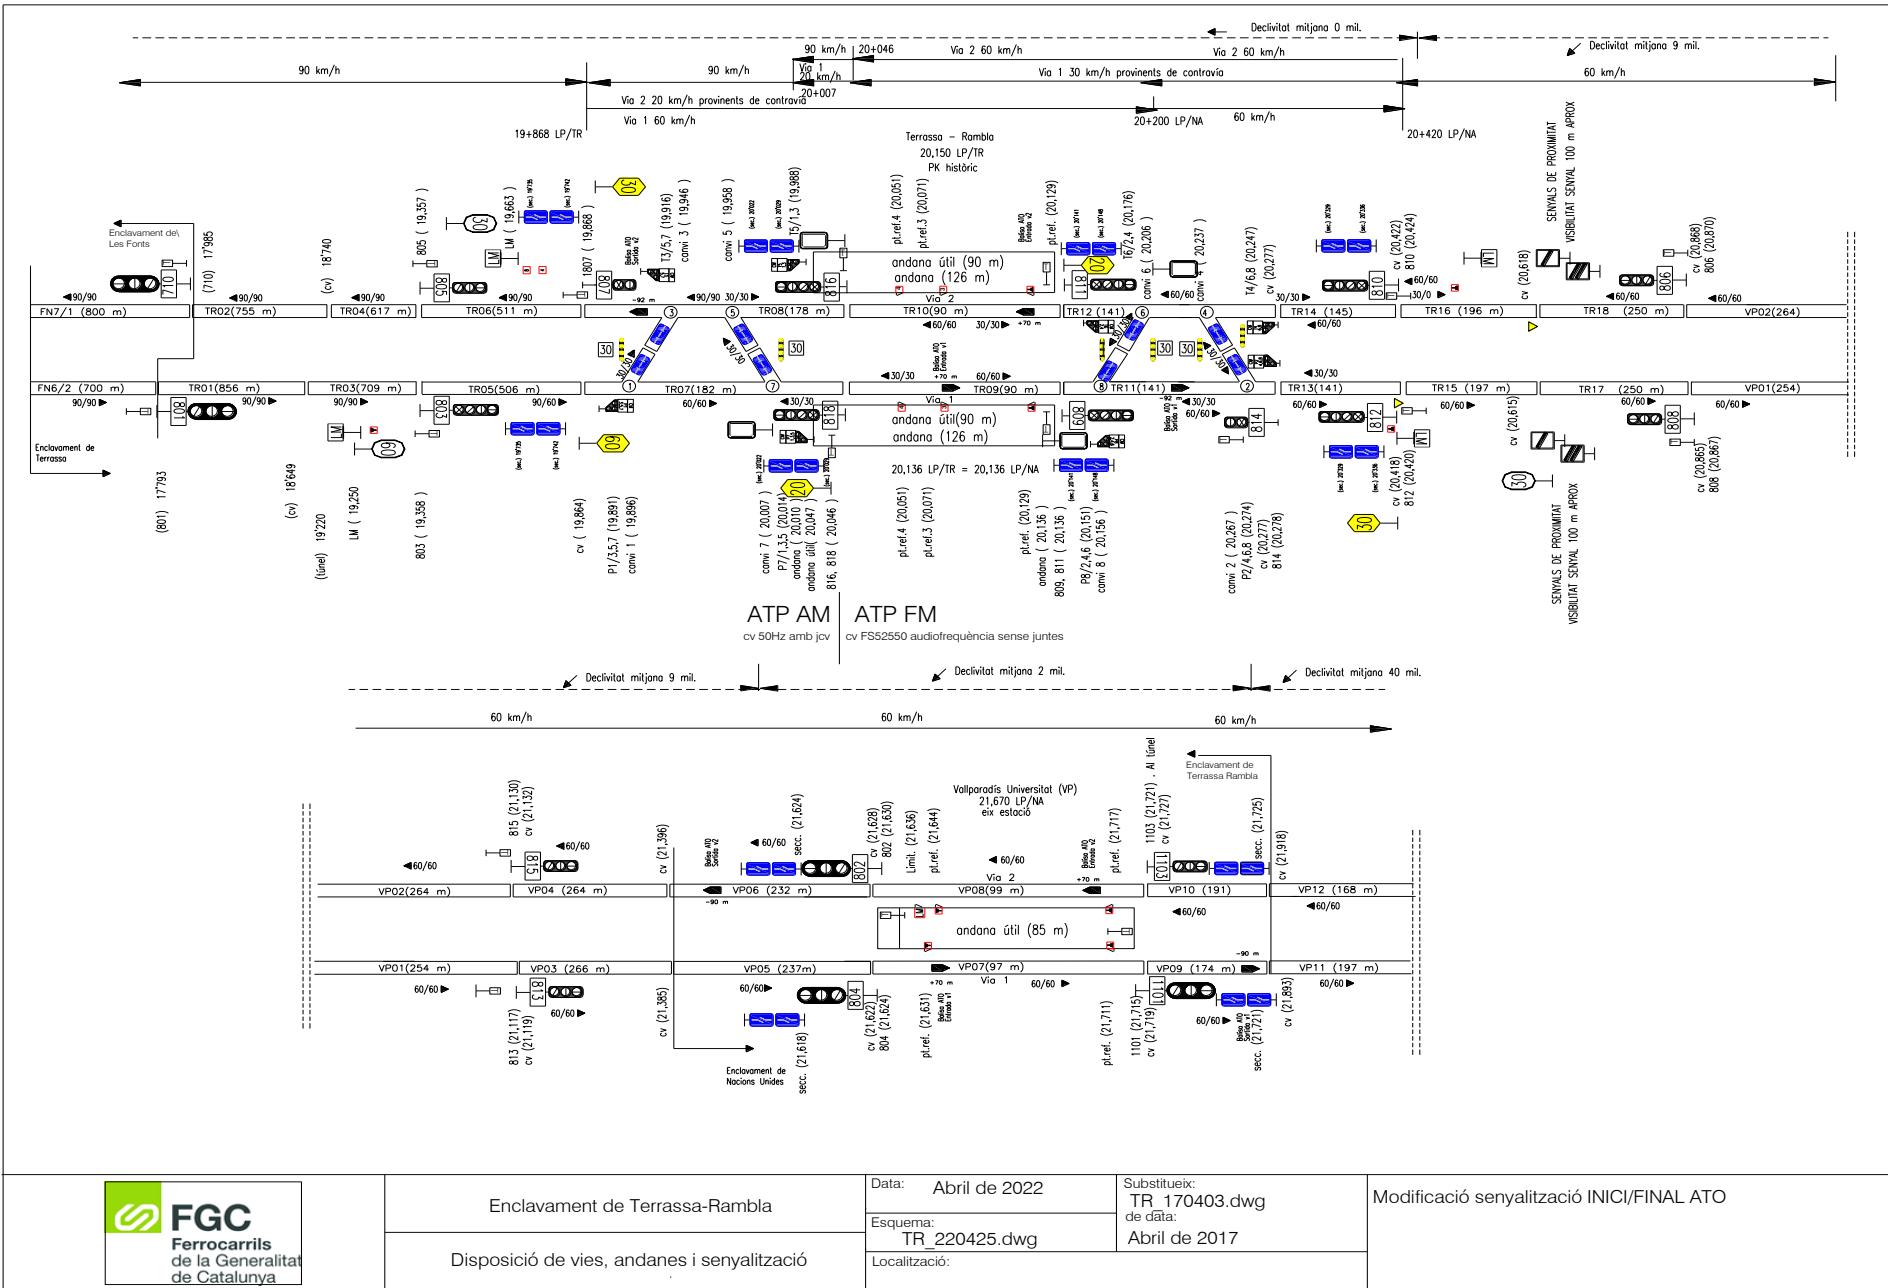


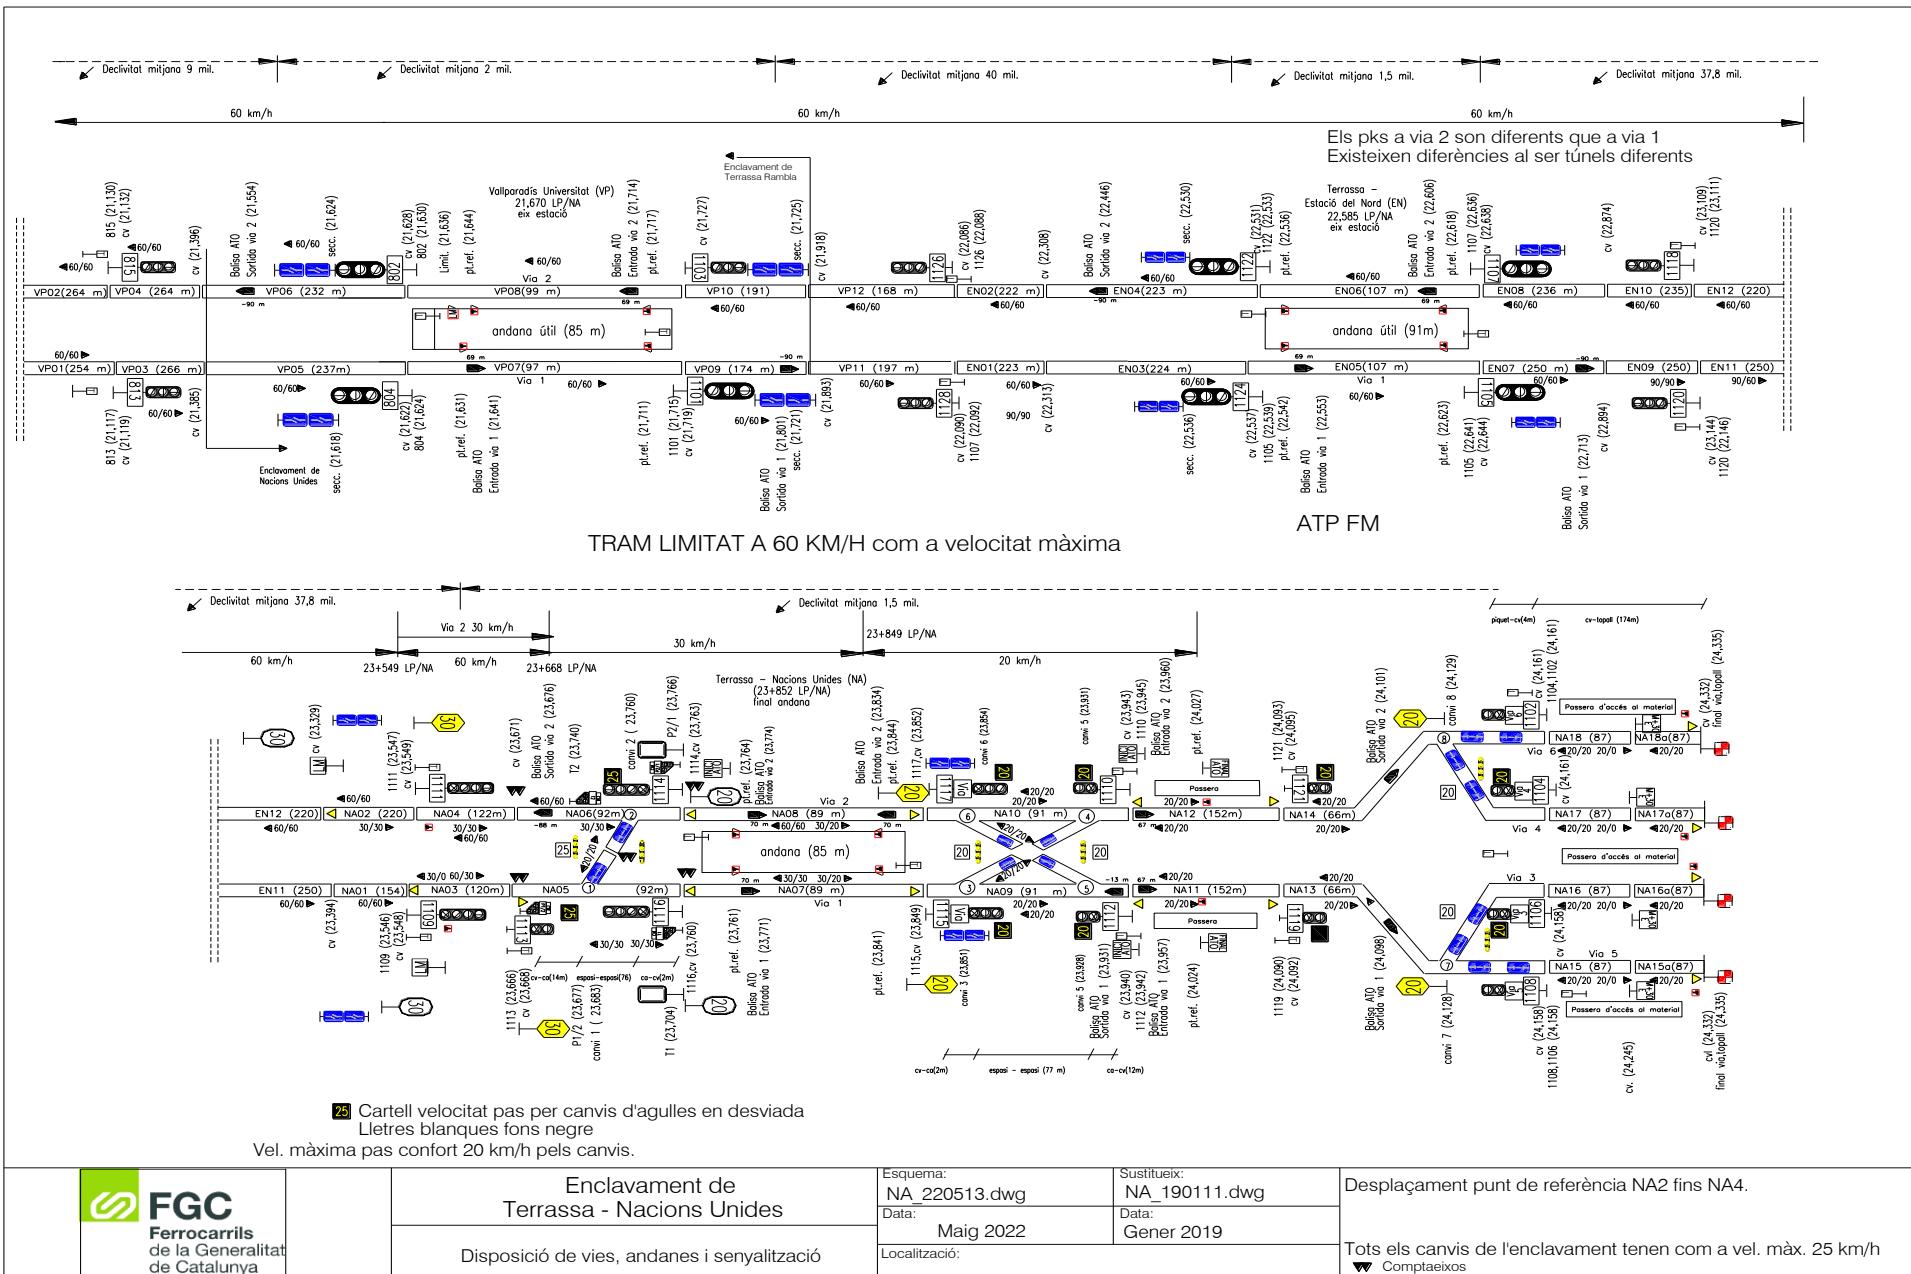

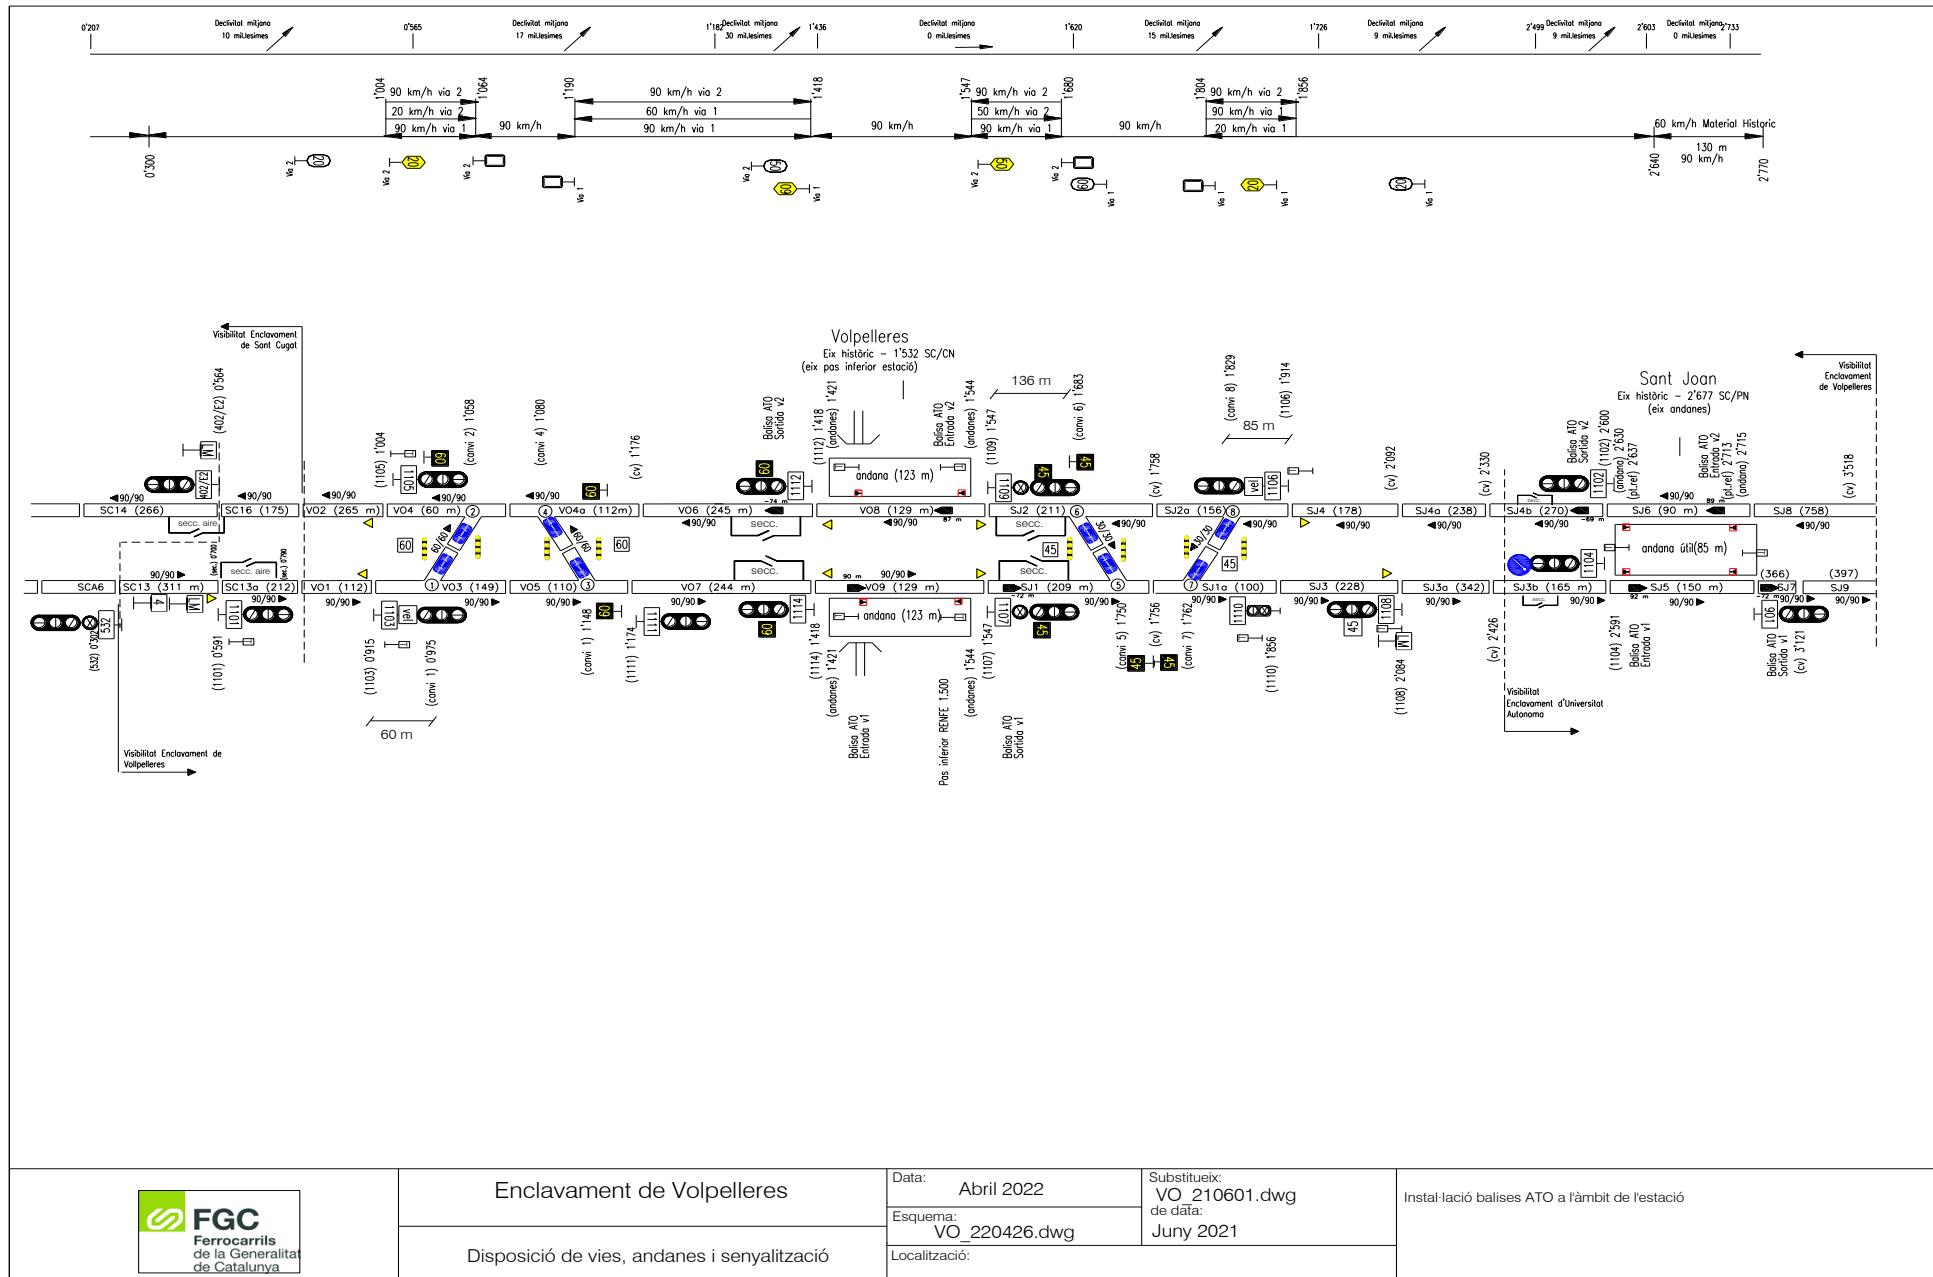

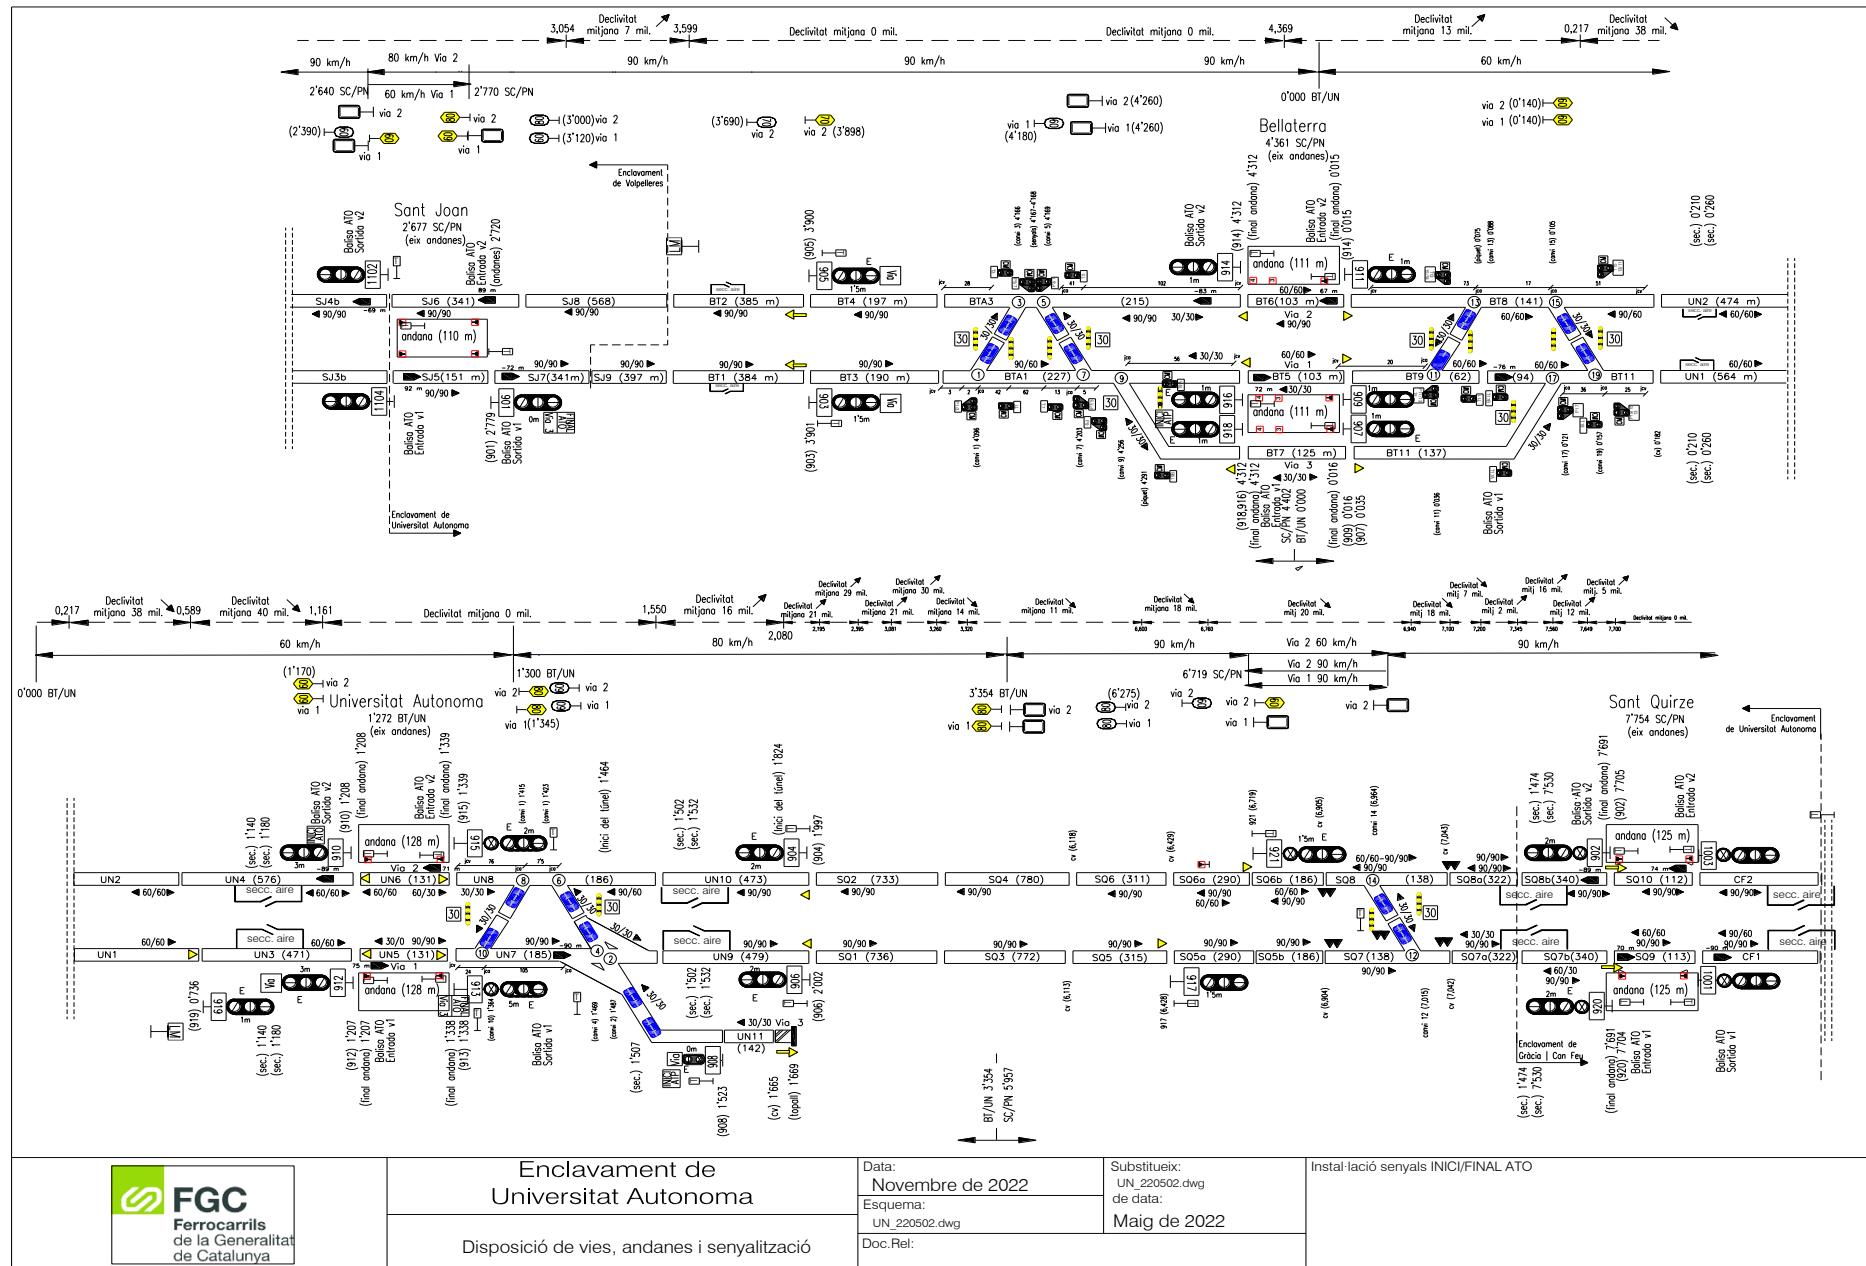

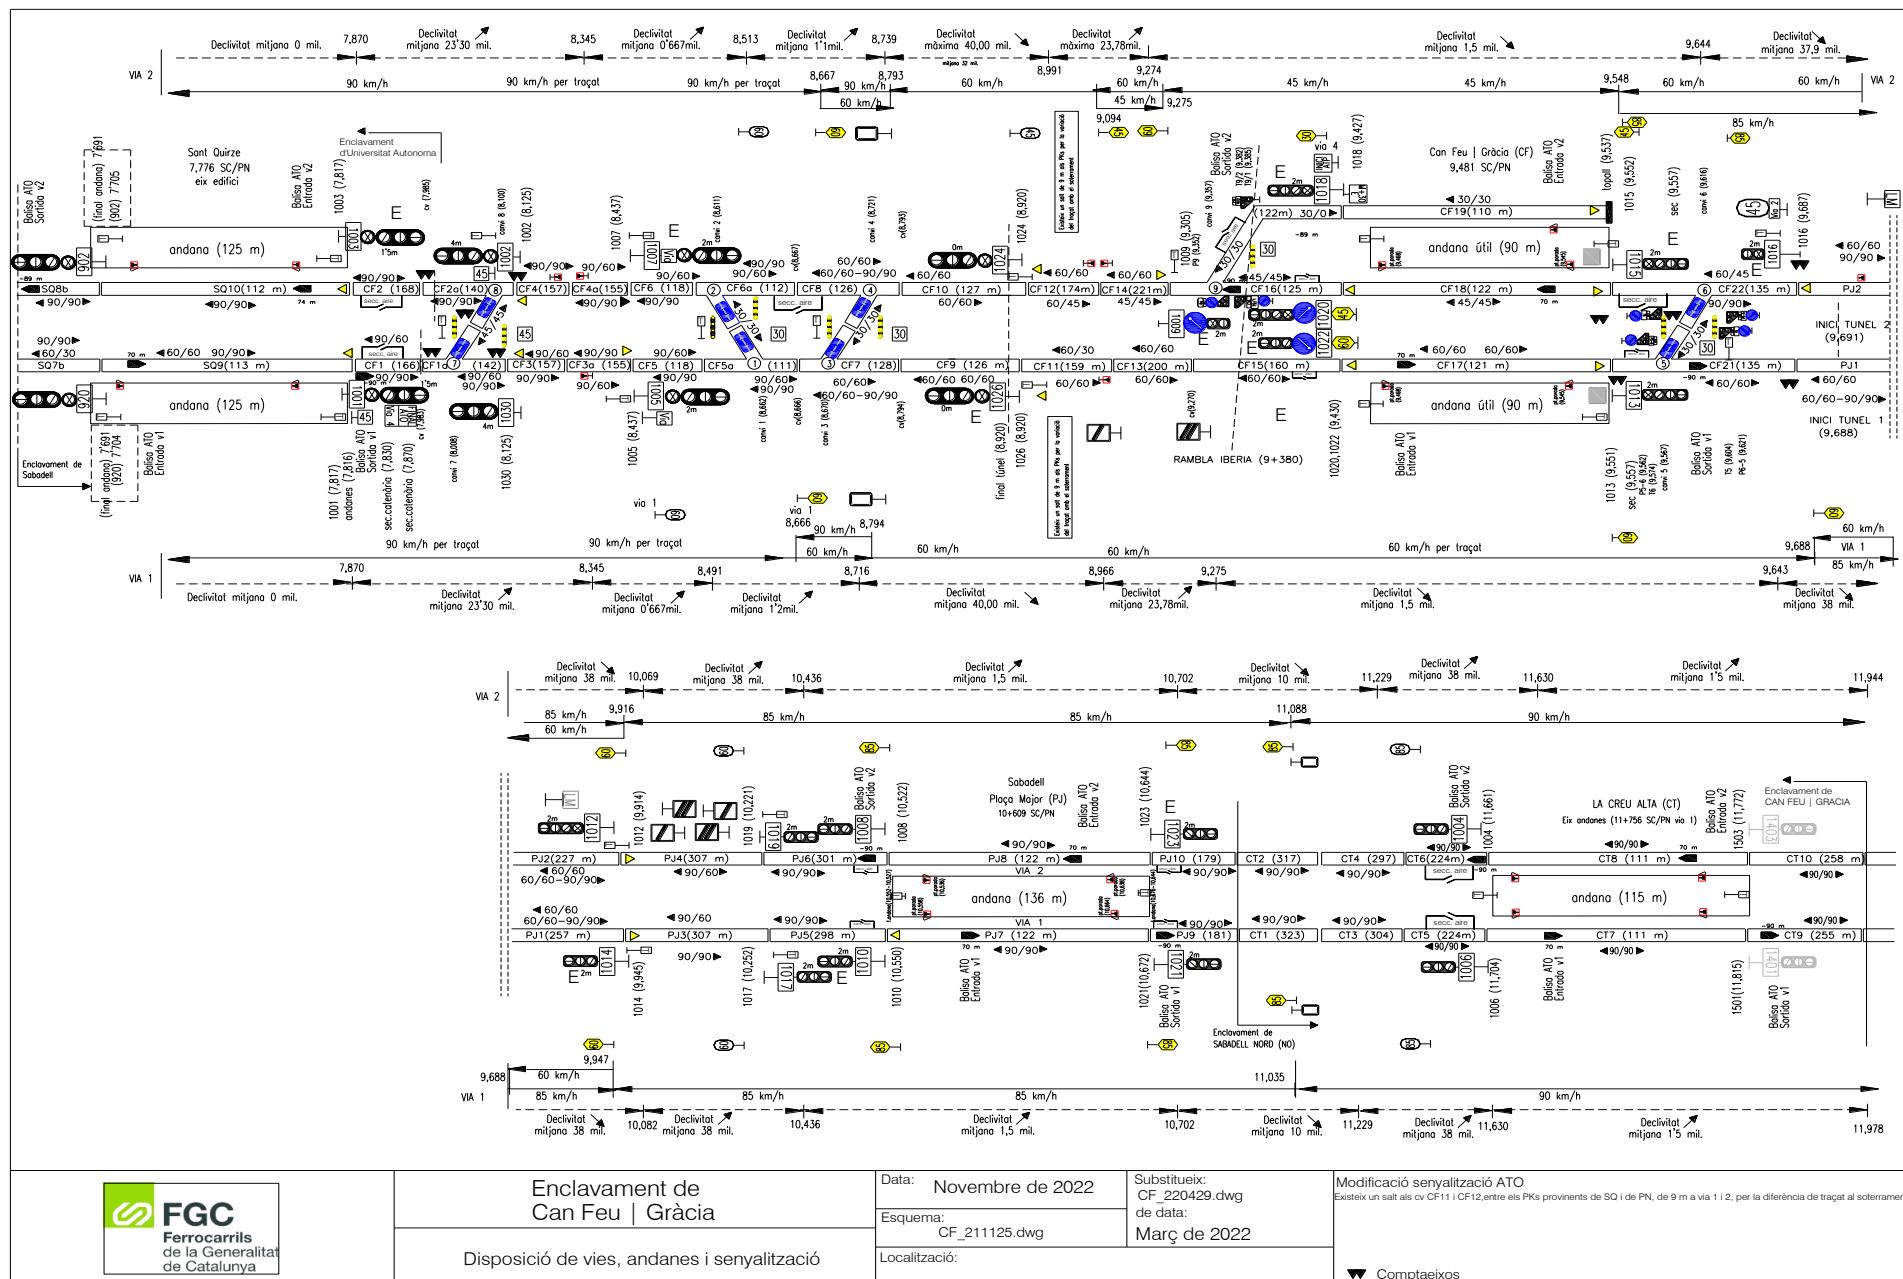

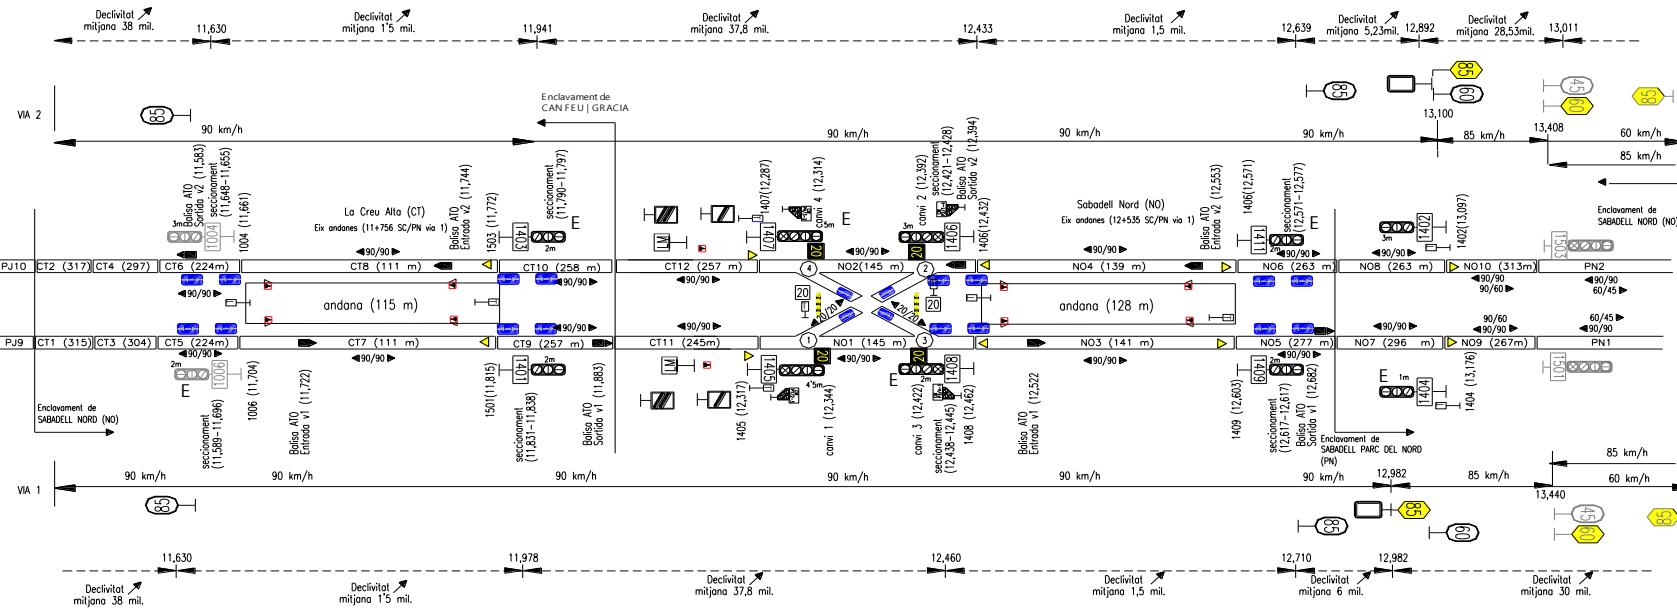

 FGC Ferrocarrils de la Generalitat de Catalunya		Enclavament de Sabadell Nord (NO)	Data: <u>Gener 2020</u>	Substitueix: NO_170612.dwg	Revisió situació seccions de catenària.
		Disposició de vies, andanes i senyalització	Esquema: <u>NO_200121.dwg</u>	de data: <u>Juny 2017</u>	

